

Stadt - Gemeinde: Kirchheim unter Teck

Landkreis: Nürtingen

Baugesuch

Bauherr Martin Hanke, Ingenieur
Kirchheim unter Teck
Paradiesstraße 21

Bauvorhaben: Umbau des bestehenden
Wohngebäudes

Grundstück: Roseggerstrasse 9

Architekt Fritz Allmendinger
Freier Architekt
Altbach/Neckar

BAUTAGEBUCH
19 70 Nr. 430

LAGEPLAN


KREIS: NÜRTINGEN
STADT: KIRCHHEIM-TECK
MARKUNG:

MASSTAB 1:500



O.W. 102 KLOSTERSTR.

O.W. 140

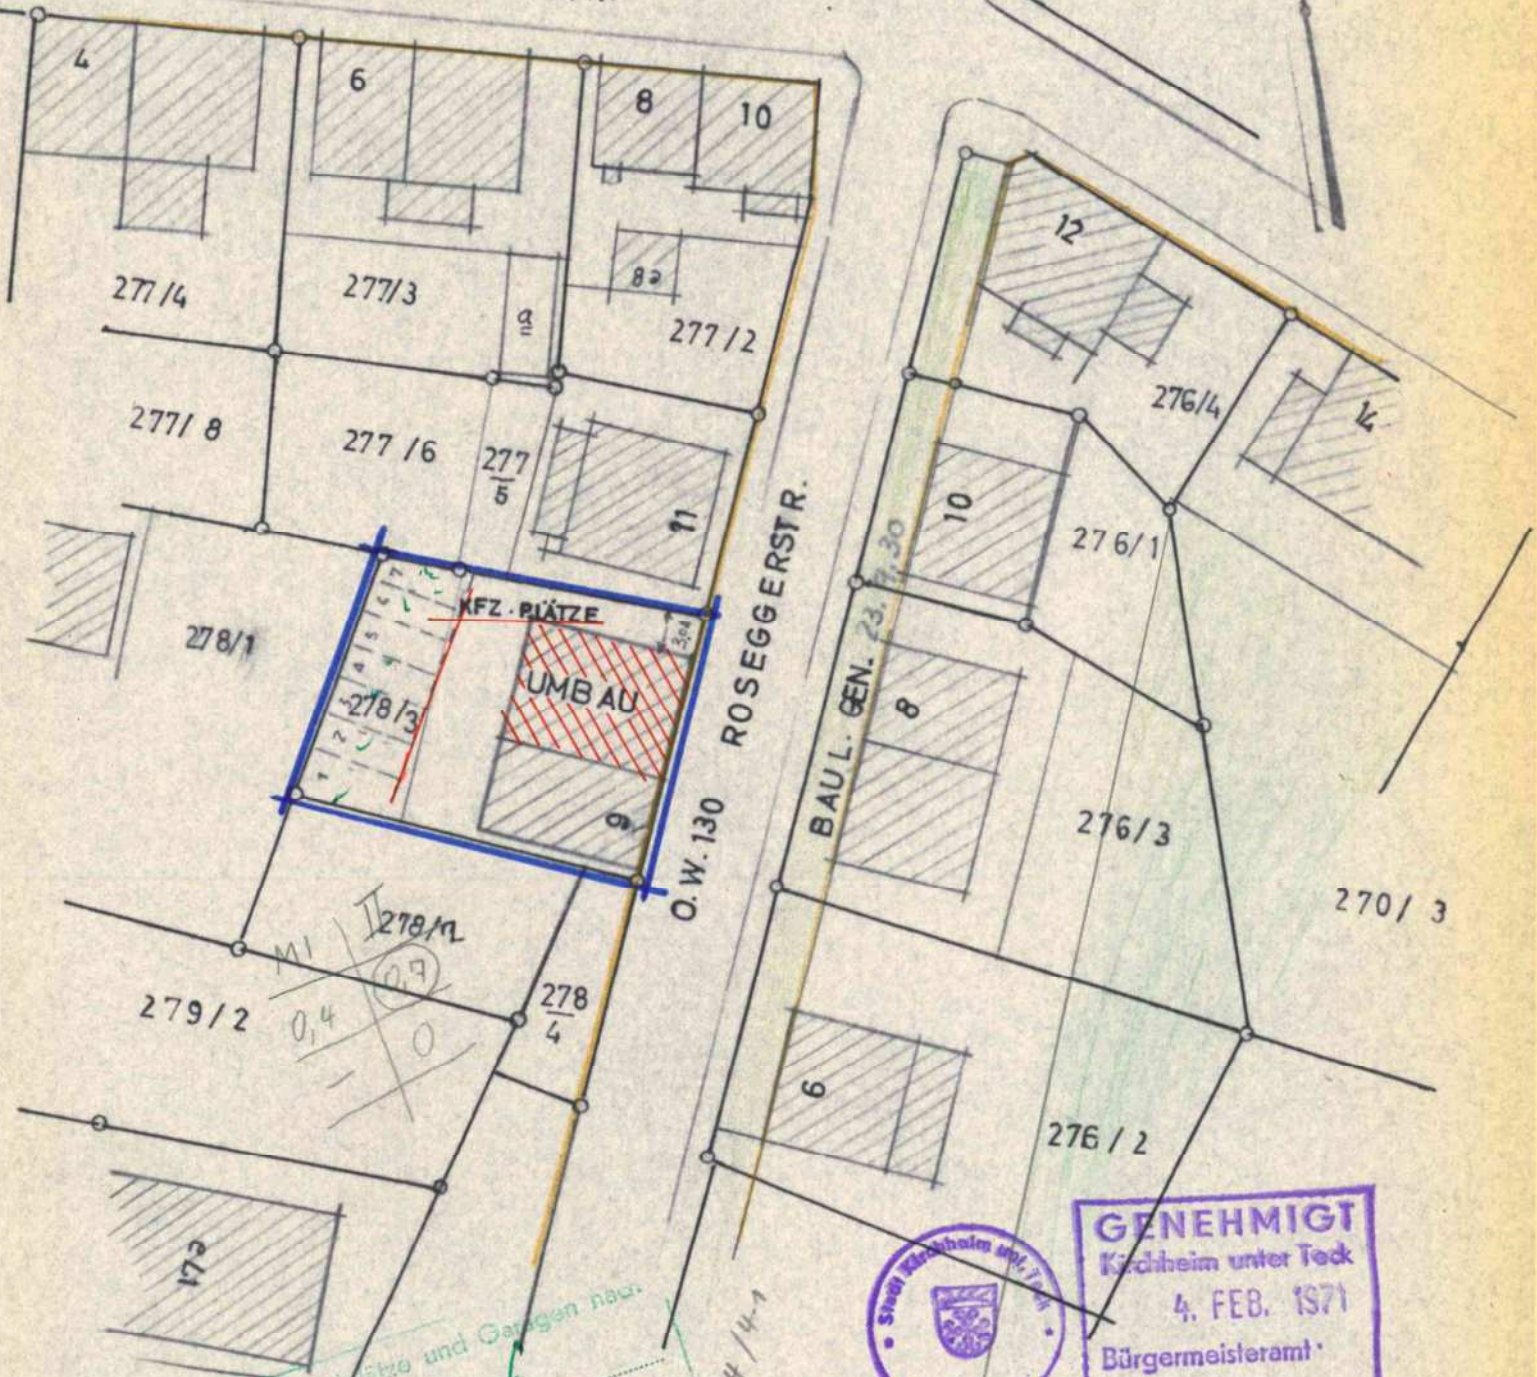

Kfz-Einzelplätze und Garagen nach
§ 3 der BauO
Erforderlich:
vorhanden:
neu zu schaffen:
6+4




GENEHMIGT
Kirchheim unter Teck
4. FEB. 1971
Bürgermeisteramt

GEFERTIGT: 5.12.70

Fritz Allmendinger
FRITZ ALLMENDINGER
ARCHITEKT
7305 ALTBACH
UHLANDWEG 21

KIRCHHEIM - TECK UMBAU ROSEGGGERSTR. 9

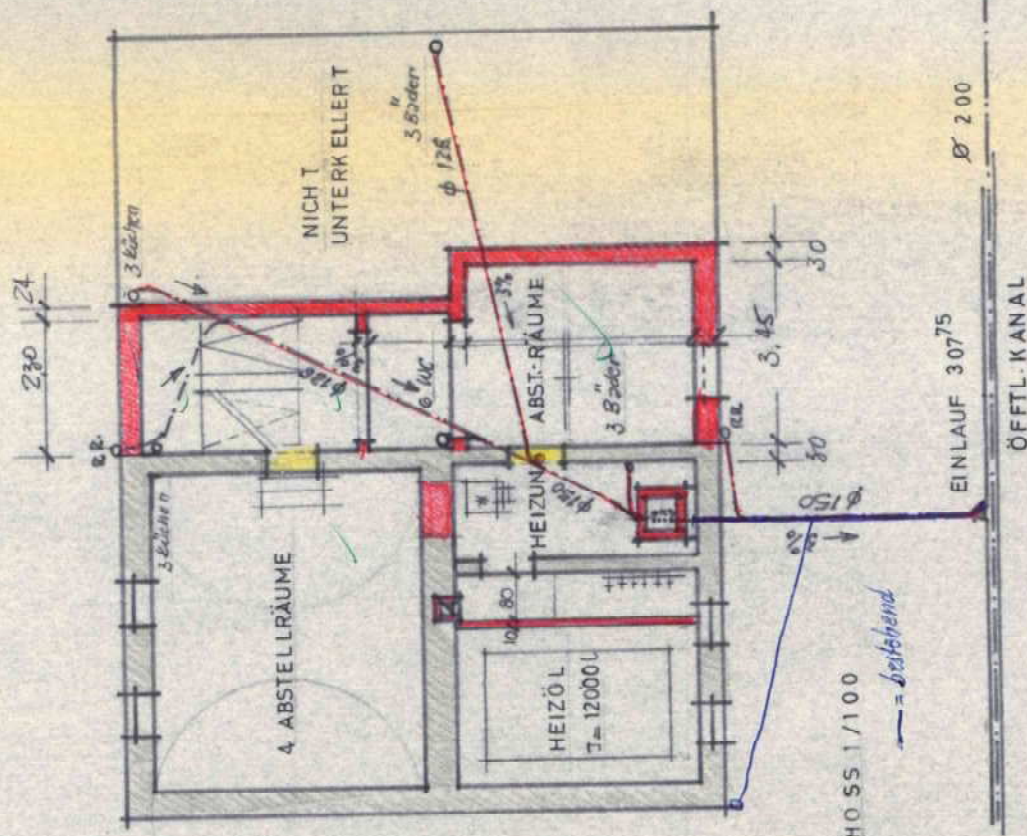


DAS UNTERGESCHOSS 1/100

= bestehend


ANERKANNT:

BAUHERR:

Paul Lohr

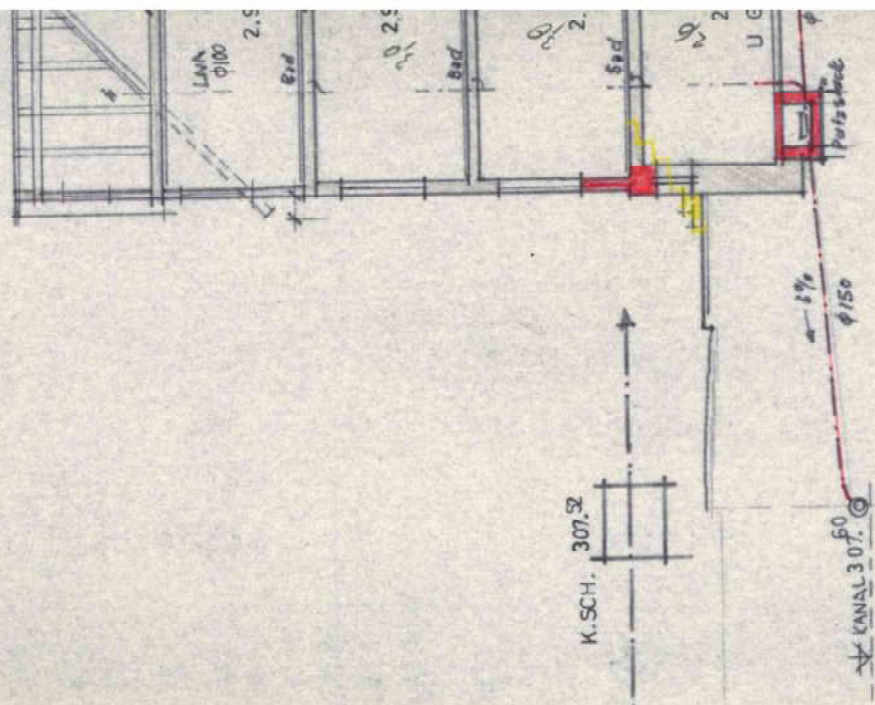

DER SCHNITT 1/100

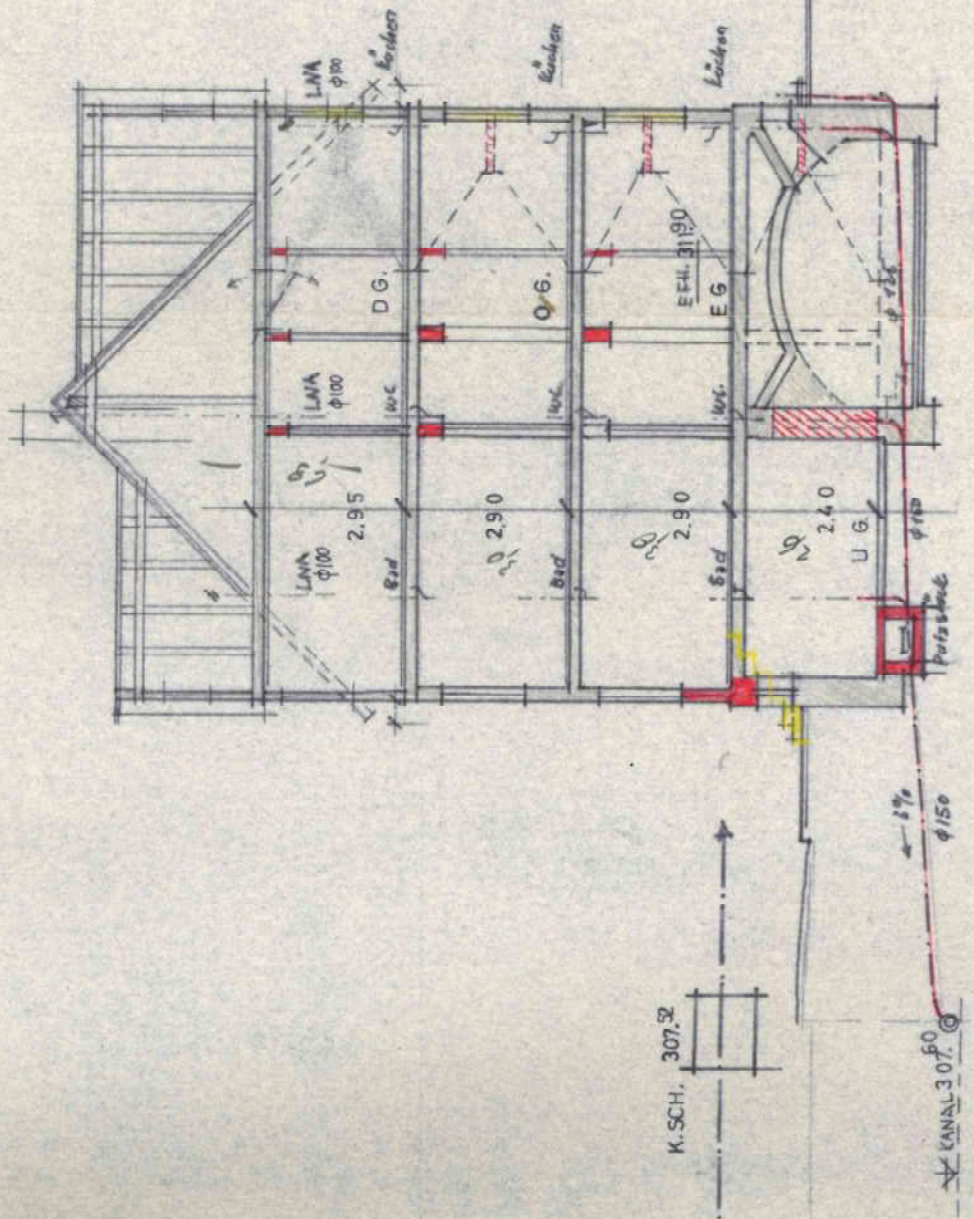

GENEHMIGT
Kirchheim unter Teck
4. FEB. 1971
Bürgermeisteramt




GEFERTIGT: 5-12-70

ARCHITEKT:

Alwin v.

12 280 115 2.30 10 2.72 14

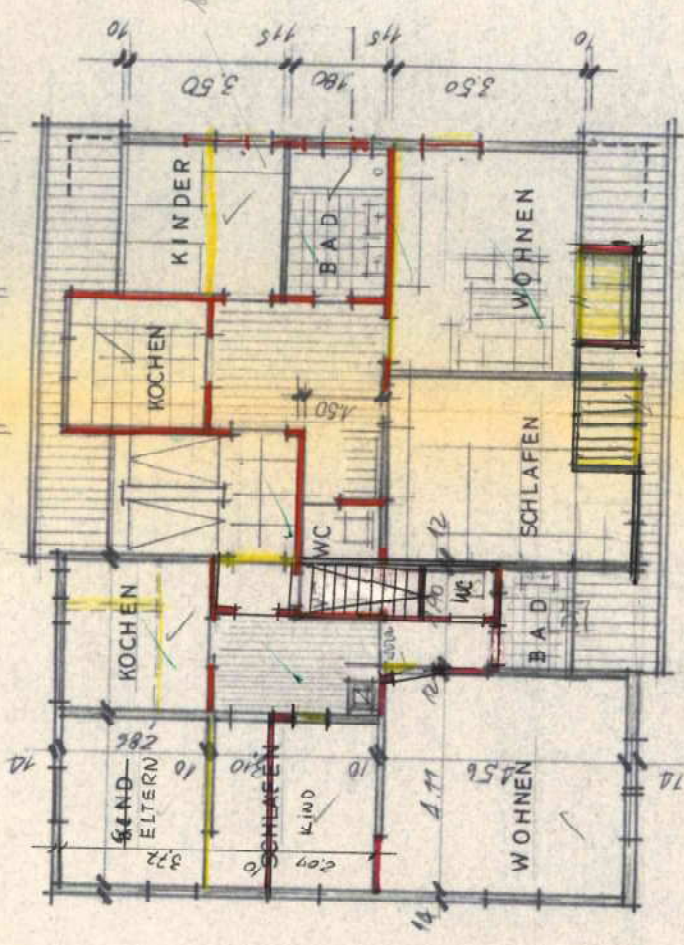

15.9.71




GENEHMIGT
Kirchheim am Teck
4. FEB. 1971
Bürgermeisteramt

GEFERTIGT: 5.12.70


ARCHITEKT:

Oliver

DAS DACHGESCHOSS 1/100


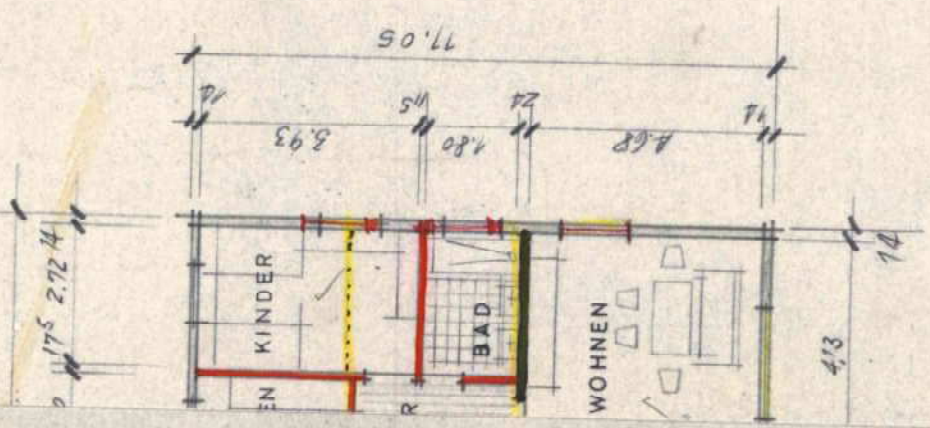


KIRCHHEIM-TECK

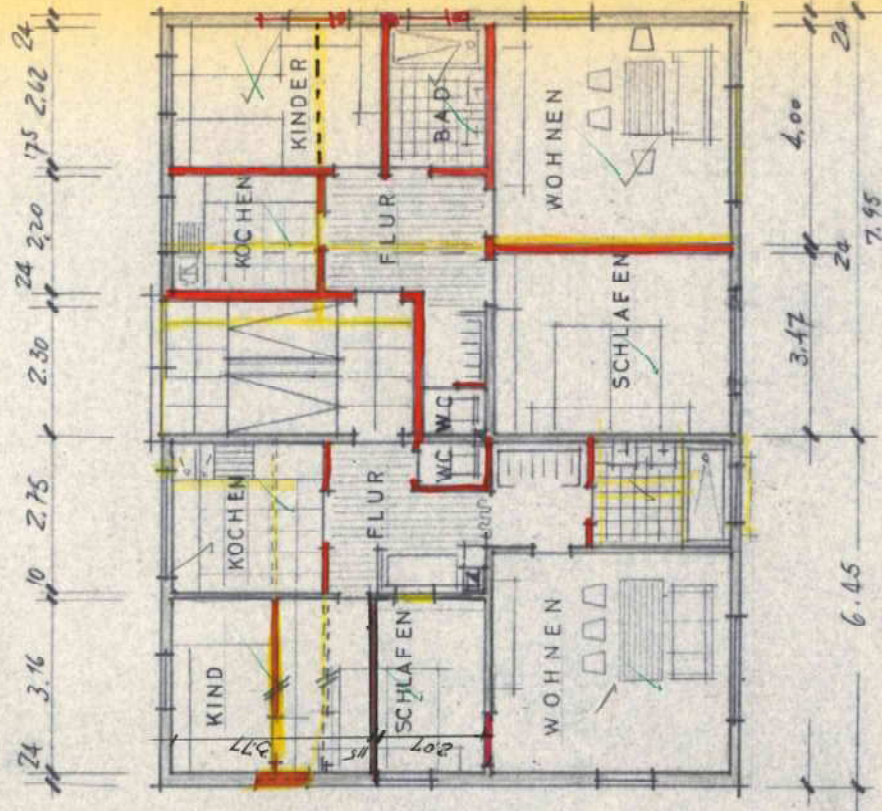


DAS ERDGESCHOSS 1/100

ANERKANT:
BAUHERR: *Karl Kuhn*

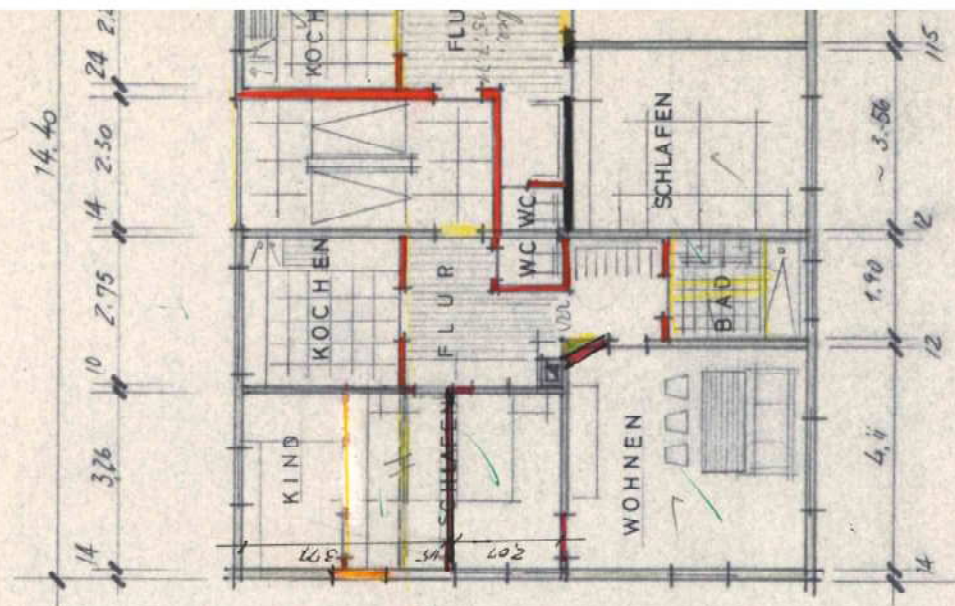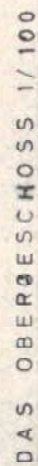

- 14,4 -

KIRCHHEIM-TECK
UMBAU ROSEGGGERSTR. 9

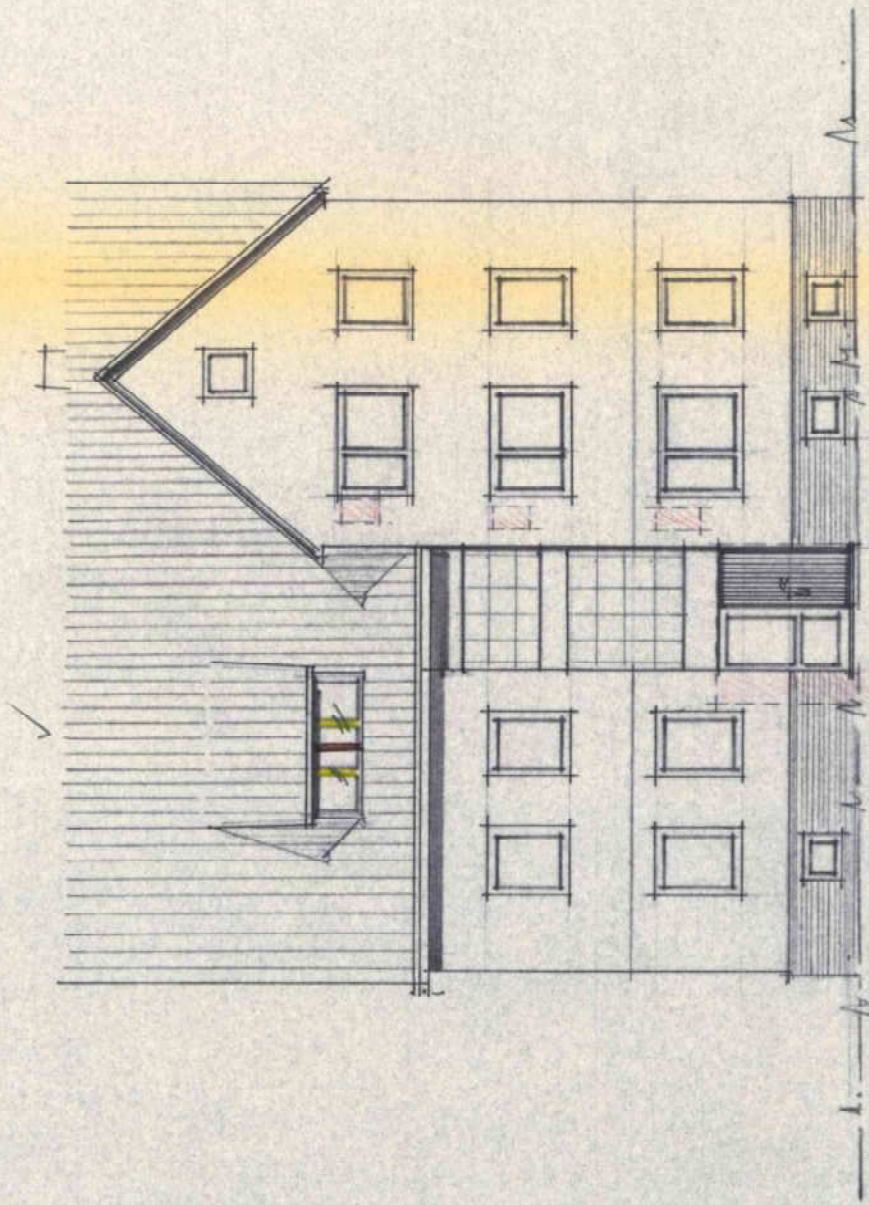


DIE WESTSEITE 1/100

ANERKANNT:
BAUHERR:

Paul Kauer

DIE NORDSEITE 1/100

STR. 9

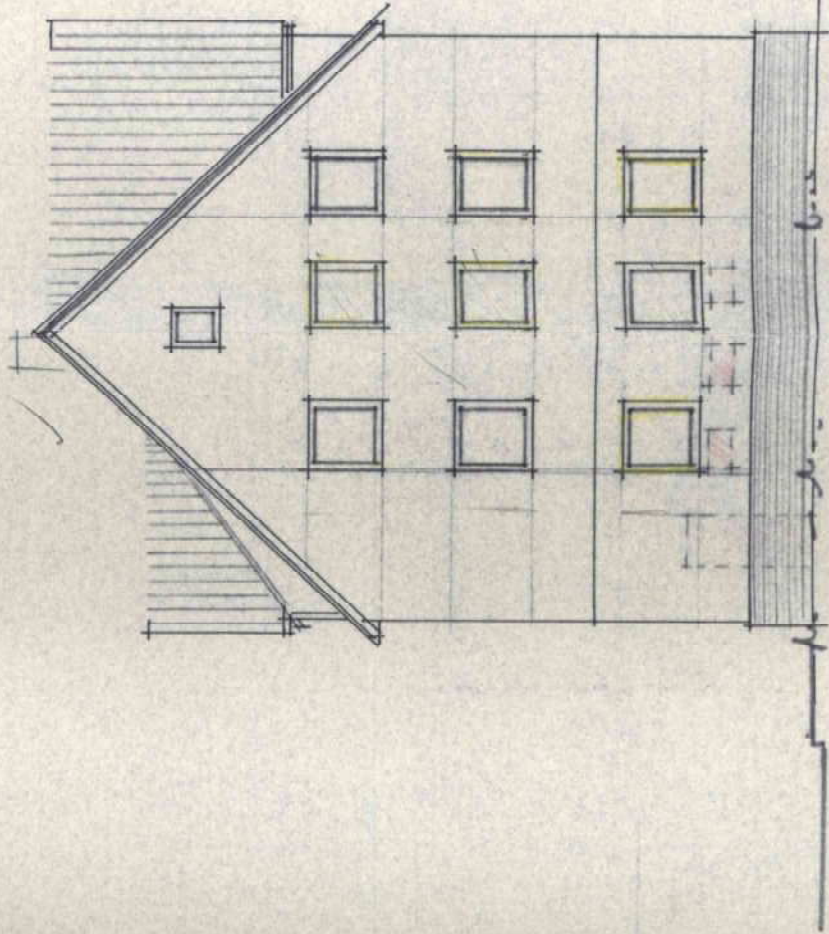

GENEHMIGT
Kirchheim unter Teck
4. FEB. 1871
Bürgermeisteramt



DIE NORDSEITE 1/100

GEFERTIGT: 5.12.70
ARCHITEKT:

Almuth S.

KIRCHHEIM - TECK
UMBAU ROSEGERSTR. 9



OSTSEITE 1 / 100

ANERKANNT:

BAUHERR:

Carl Lohm

GEFERTIGT: 5.12.70

ARCHITEKT:

Alm

GENEHMIGT

Kirchheim unter Teck

4. FEB. 1971

Bürgermeisteramt

