
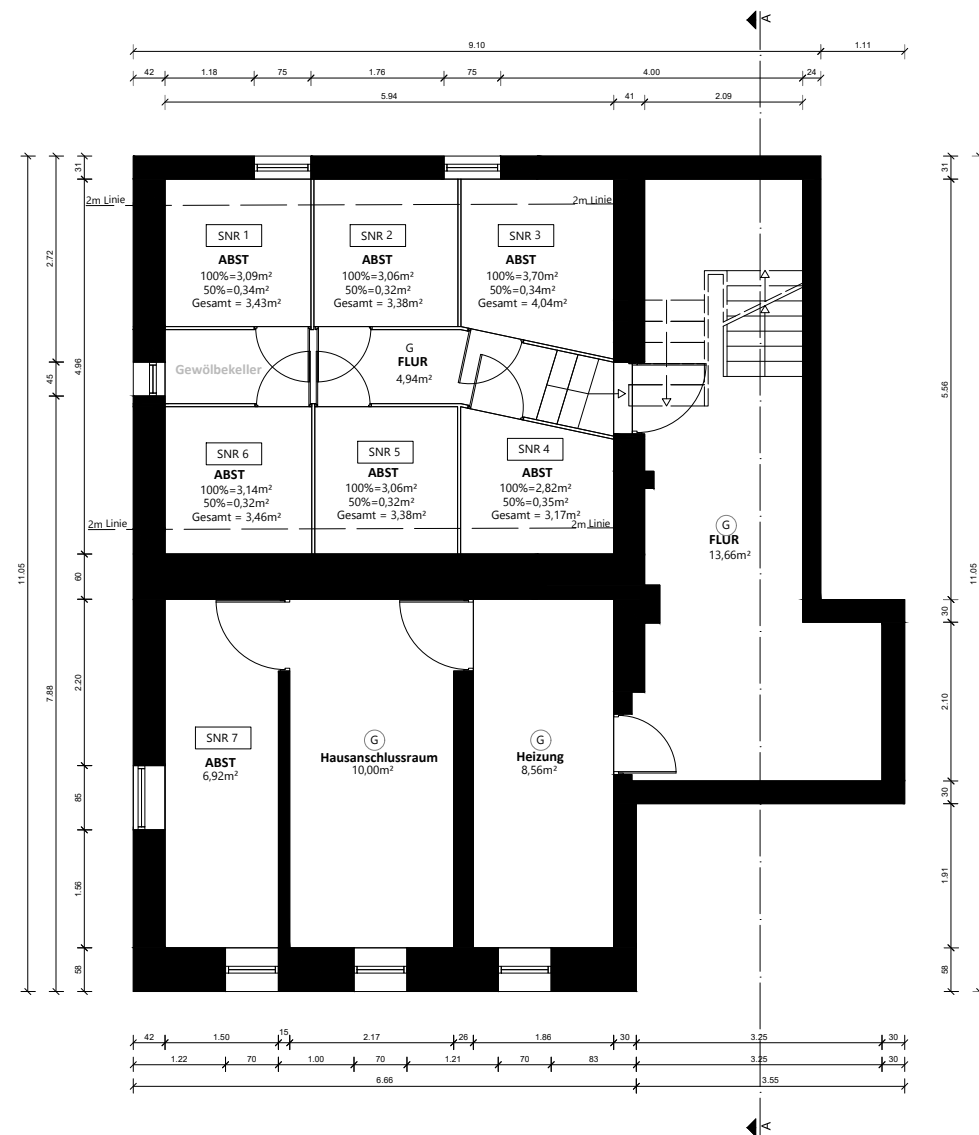


Planstand: 08.06.2026

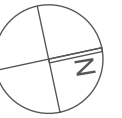

TEILUNGSPLAN

Untergeschoss

Art und Ort
des Vorhabens: Aufteilung eines bestehenden Wohngebäudes mit 7 Wohneinheiten
Roseggerstraße 9
73230 Kirchheim unter Teck
Flst.-Nr.: 278/3

Bauherr u.
Antragsteller: Württemberger Wohnkonzepte GmbH
Jesinger Str. 66
73230 Kirchheim unter Teck
Vertreten durch die Geschäftsführung: Dorothee Hahn & Marco Hans

Entwurfsverfasser:





jps architects
Jean Pierre Schellhaas
Architekt
Krokusstraße 3
71034 Böblingen
Mitglied der AKBW

jp@jps-architects.com
0157 / 39 22 86 22

M 1:100

Planstand: 08.06.2026

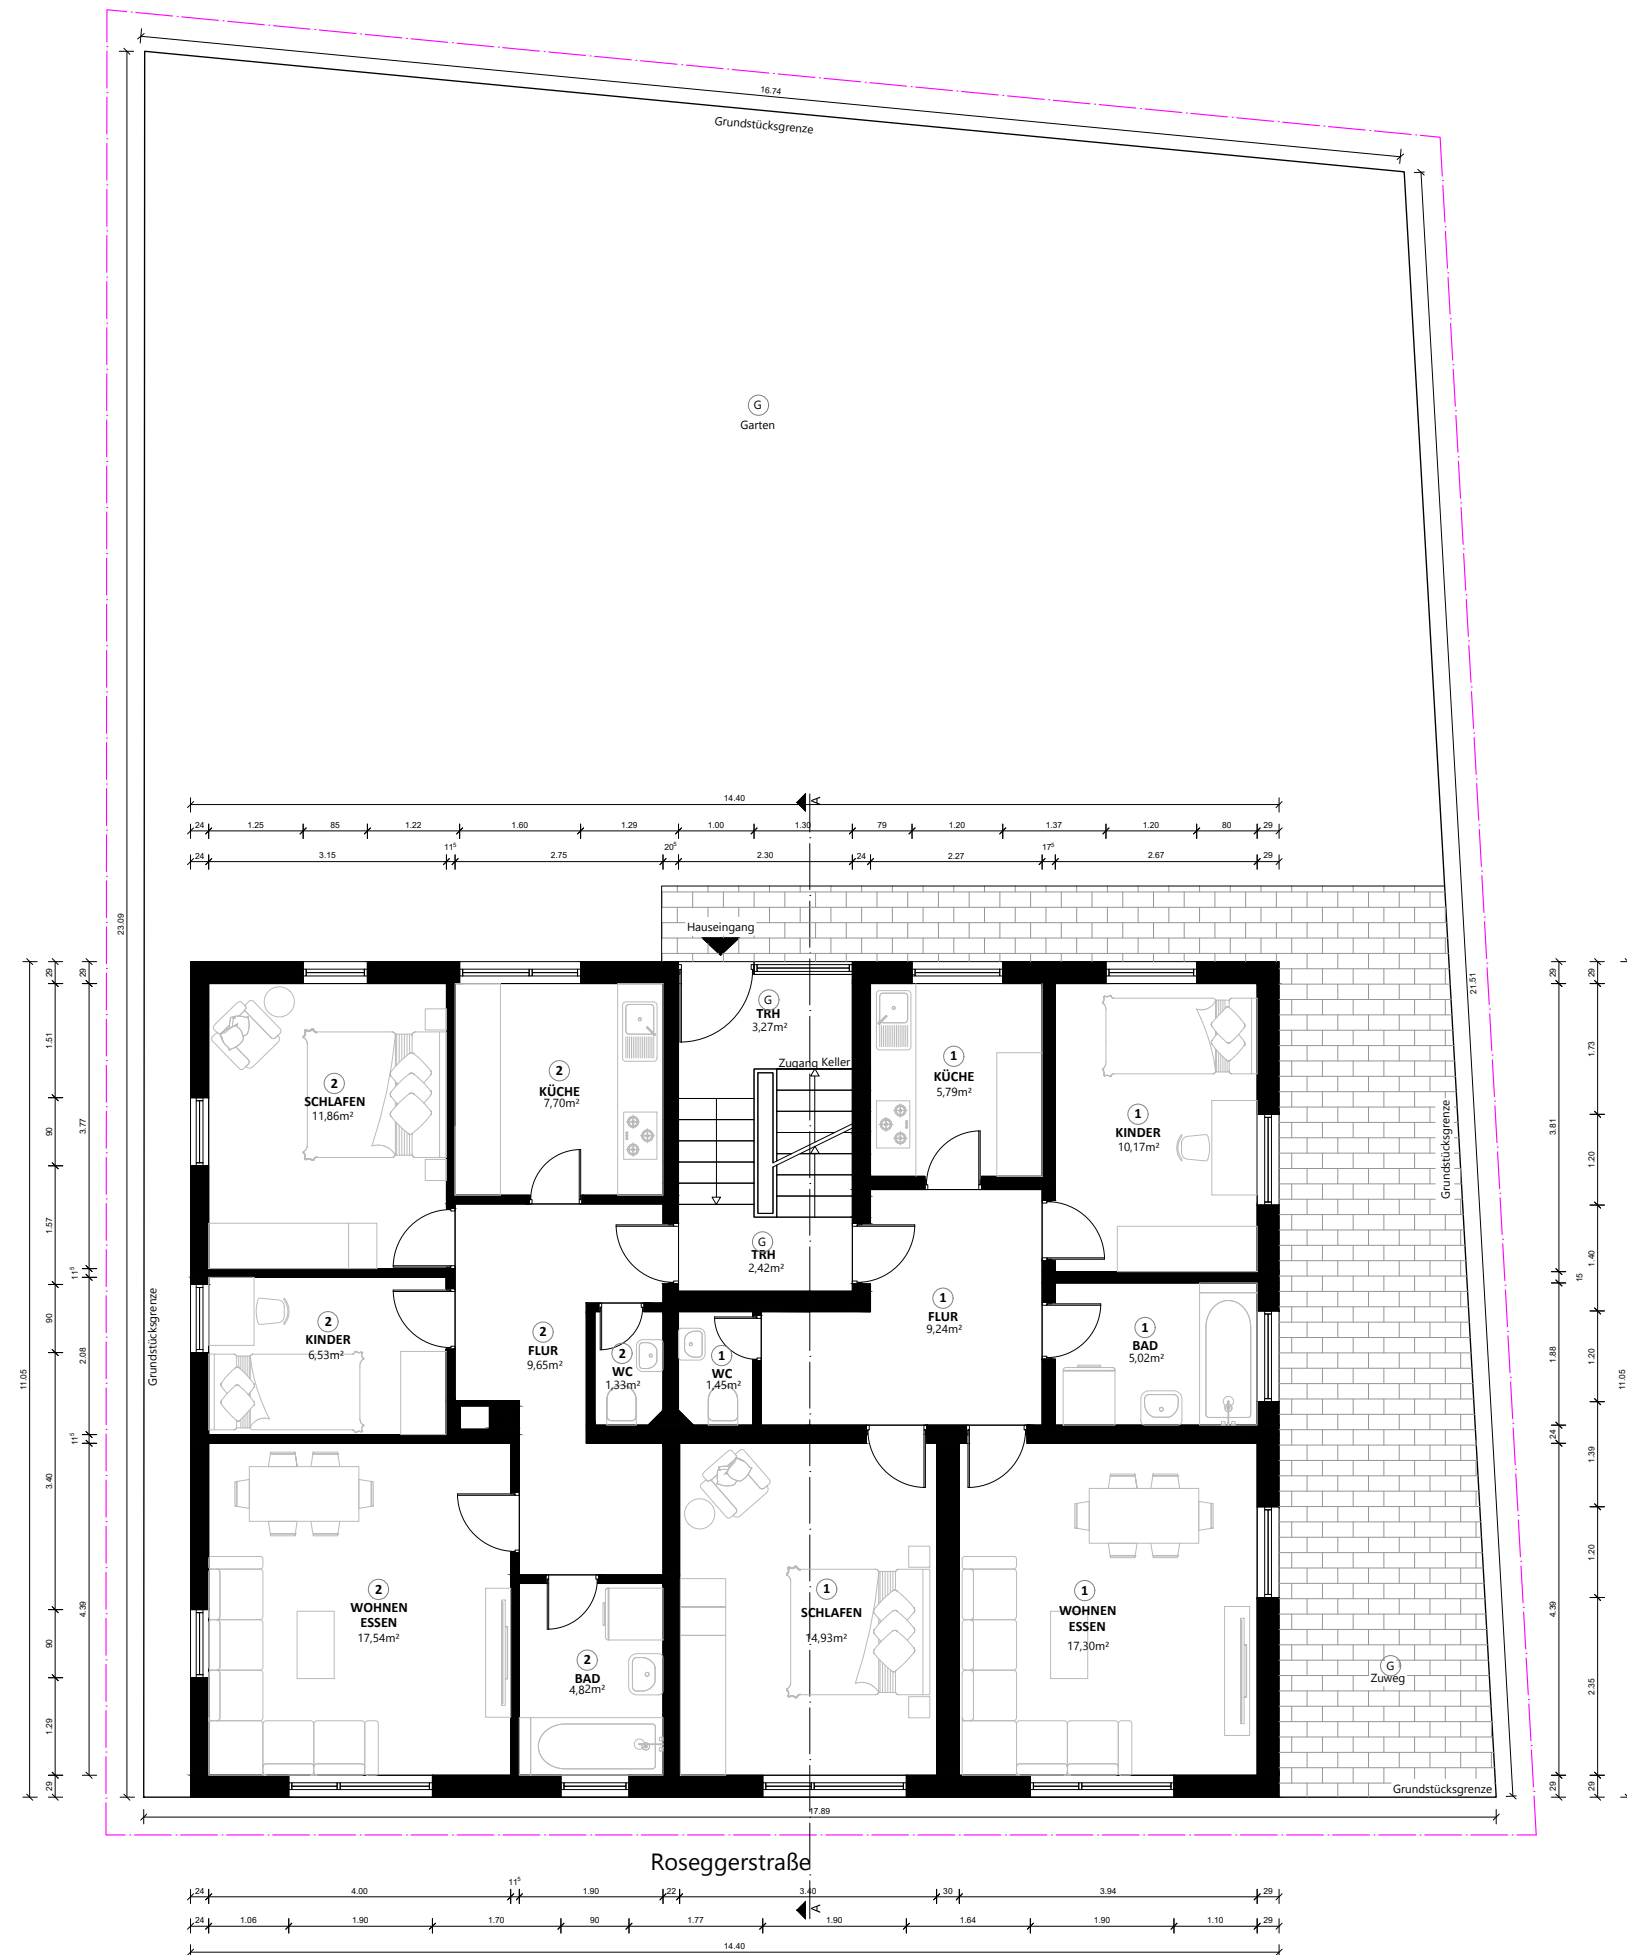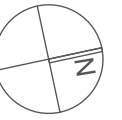

TEILUNGSPLAN

Erdgeschoss mit Umgebung

Art und Ort
des Vorhabens: Aufteilung eines bestehenden Wohngebäudes mit 7 Wohneinheiten
Roseggerstraße 9
73230 Kirchheim unter Teck
Flst.-Nr.: 278/3

Bauherr u.
Antragsteller: Württemberger Wohnkonzepte GmbH
Jesinger Str. 66
73230 Kirchheim unter Teck
Vertreten durch die Geschäftsführung: Dorothee Hahn & Marco Hans

Entwurfsverfasser:





jps architects
Jean Pierre Schellhaas
Architekt
Krokusstraße 3
71034 Böblingen
Mitglied der AKBW

jp@jps-architects.com
0157 / 39 22 86 22

M 1:100

Planstand: 08.06.2026

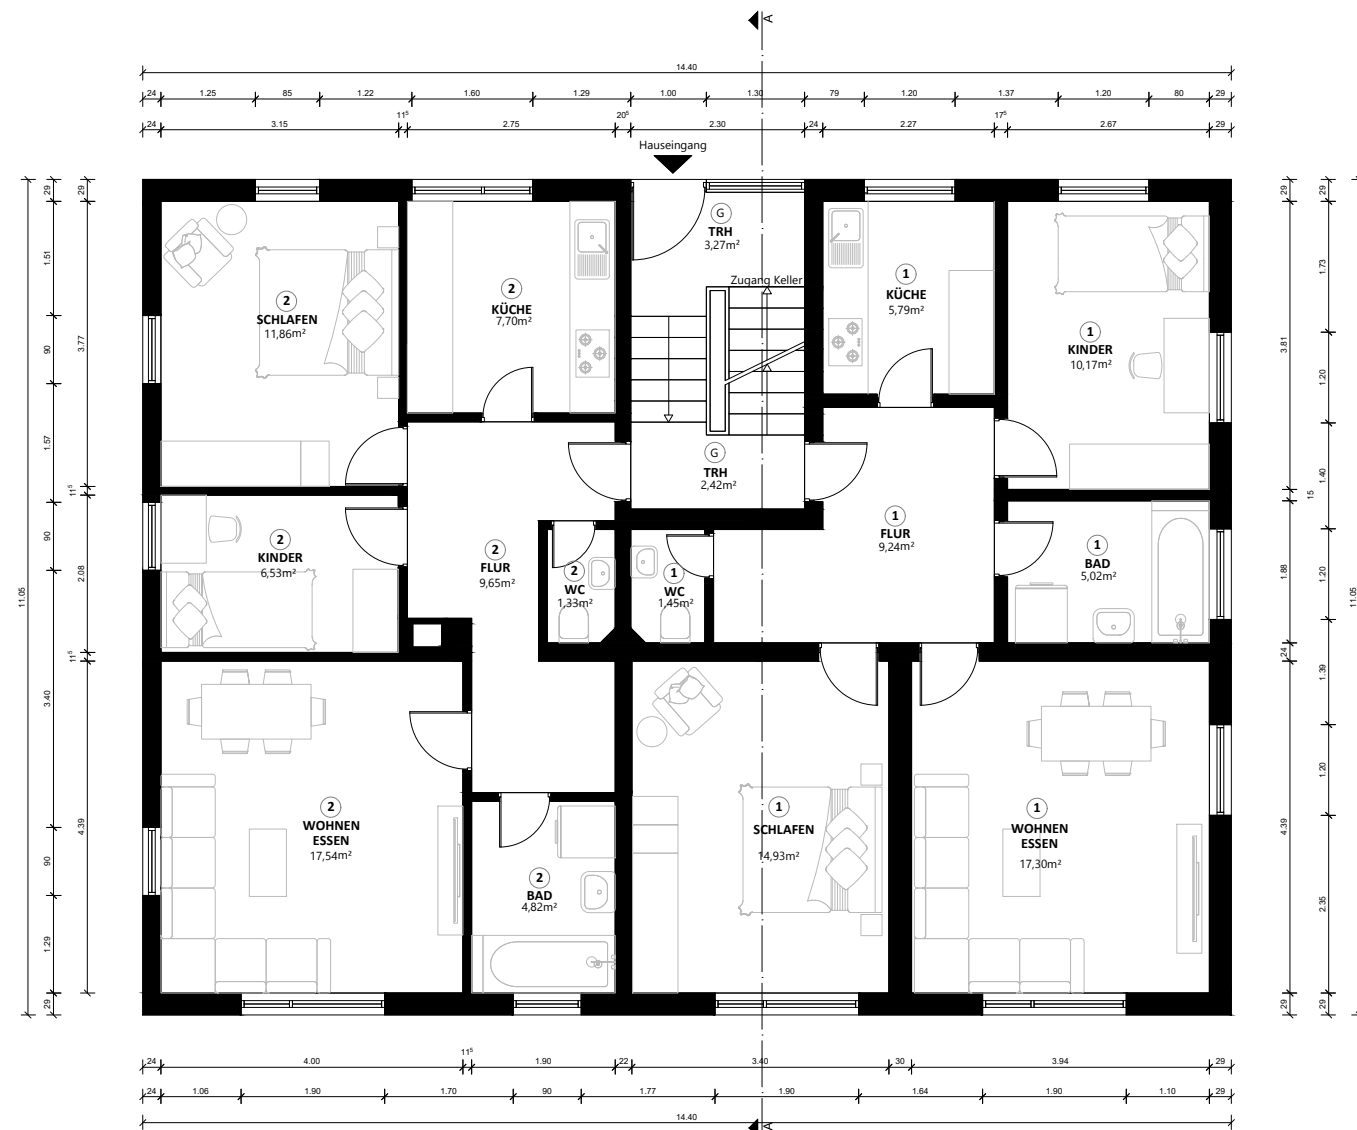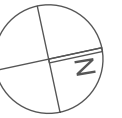

TEILUNGSPLAN

Erdgeschoss

Art und Ort des Vorhabens: Aufteilung eines bestehenden Wohngebäudes mit 7 Wohneinheiten
Roseggerstraße 9
73230 Kirchheim unter Teck
Flst.-Nr.: 278/3

Bauherr u. Antragsteller: Württemberger Wohnkonzepte GmbH
Jesinger Str. 66
73230 Kirchheim unter Teck
Vertreten durch die Geschäftsführung: Dorothee Hahn & Marco Hans

Entwurfsverfasser:





jps architects
Jean Pierre Schellhaas
Architekt
Krokusstraße 3
71034 Böblingen
Mitglied der AKBW

jp@jps-architects.com
0157 / 39 22 86 22

M 1:100

Planstand: 08.06.2026

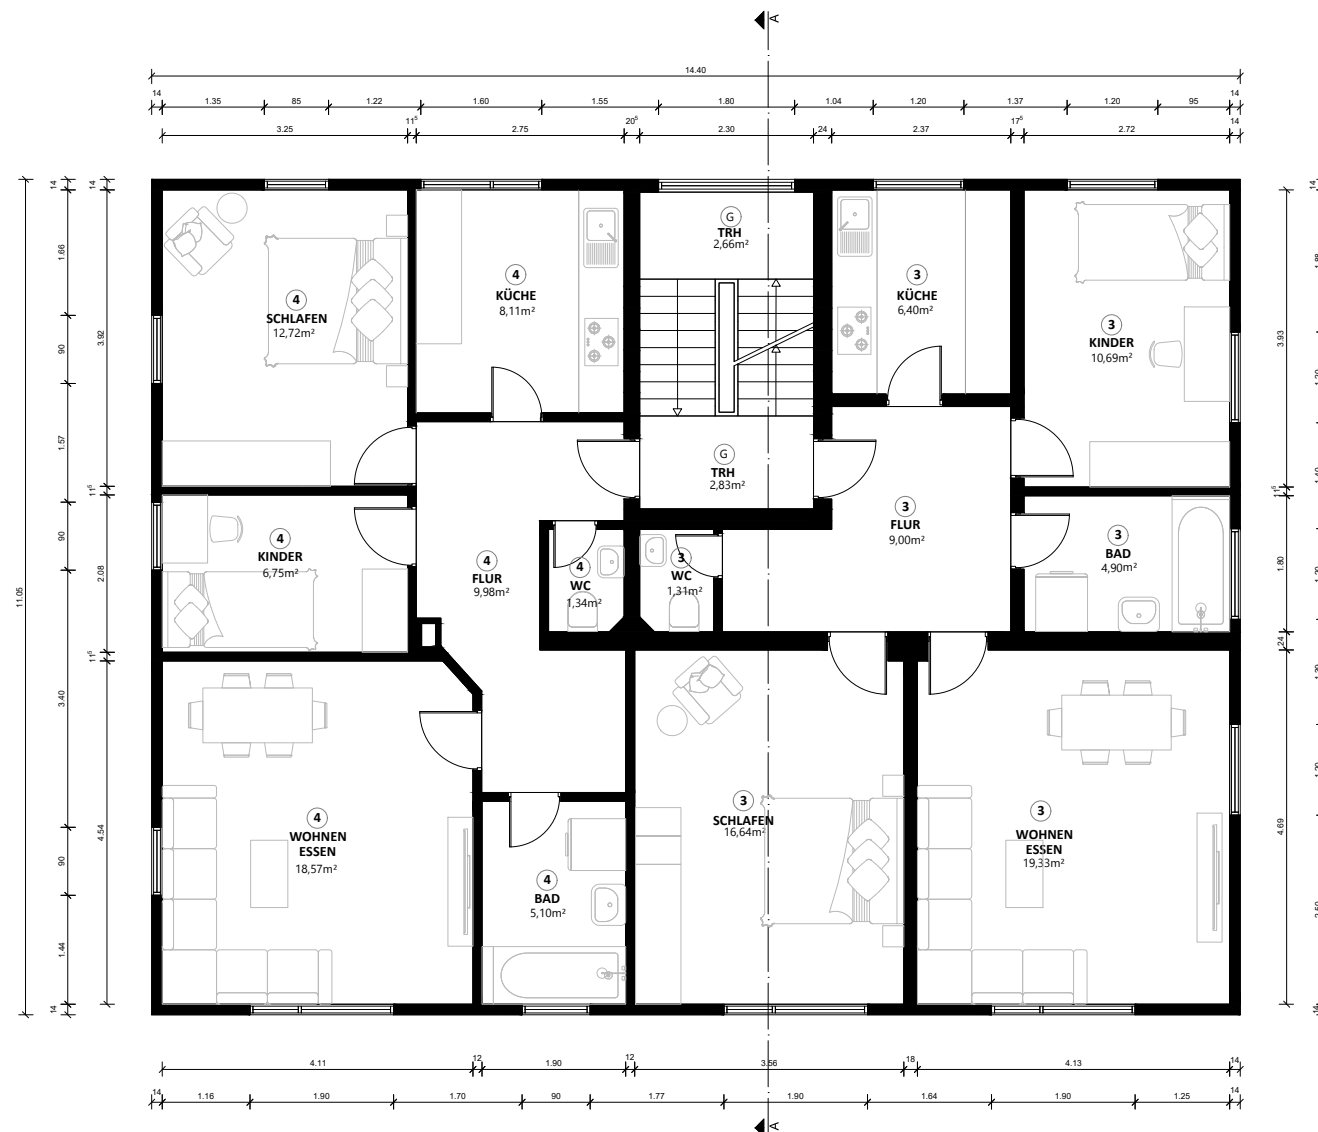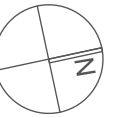

TEILUNGSPLAN

1. Obergeschoss

Art und Ort
des Vorhabens: Aufteilung eines bestehenden Wohngebäudes mit 7 Wohneinheiten
Roseggerstraße 9
73230 Kirchheim unter Teck
Flst.-Nr.: 278/3

Bauherr u.
Antragsteller: Württemberger Wohnkonzepte GmbH
Jesinger Str. 66
73230 Kirchheim unter Teck
Vertreten durch die Geschäftsführung: Dorothee Hahn & Marco Hans

Entwurfsverfasser:





jps architects
Jean Pierre Schellhaas
Architekt
Krokusstraße 3
71034 Böblingen
Mitglied der AKBW

jp@jps-architects.com
0157 / 39 22 86 22

M 1:100

Planstand: 08.06.2026

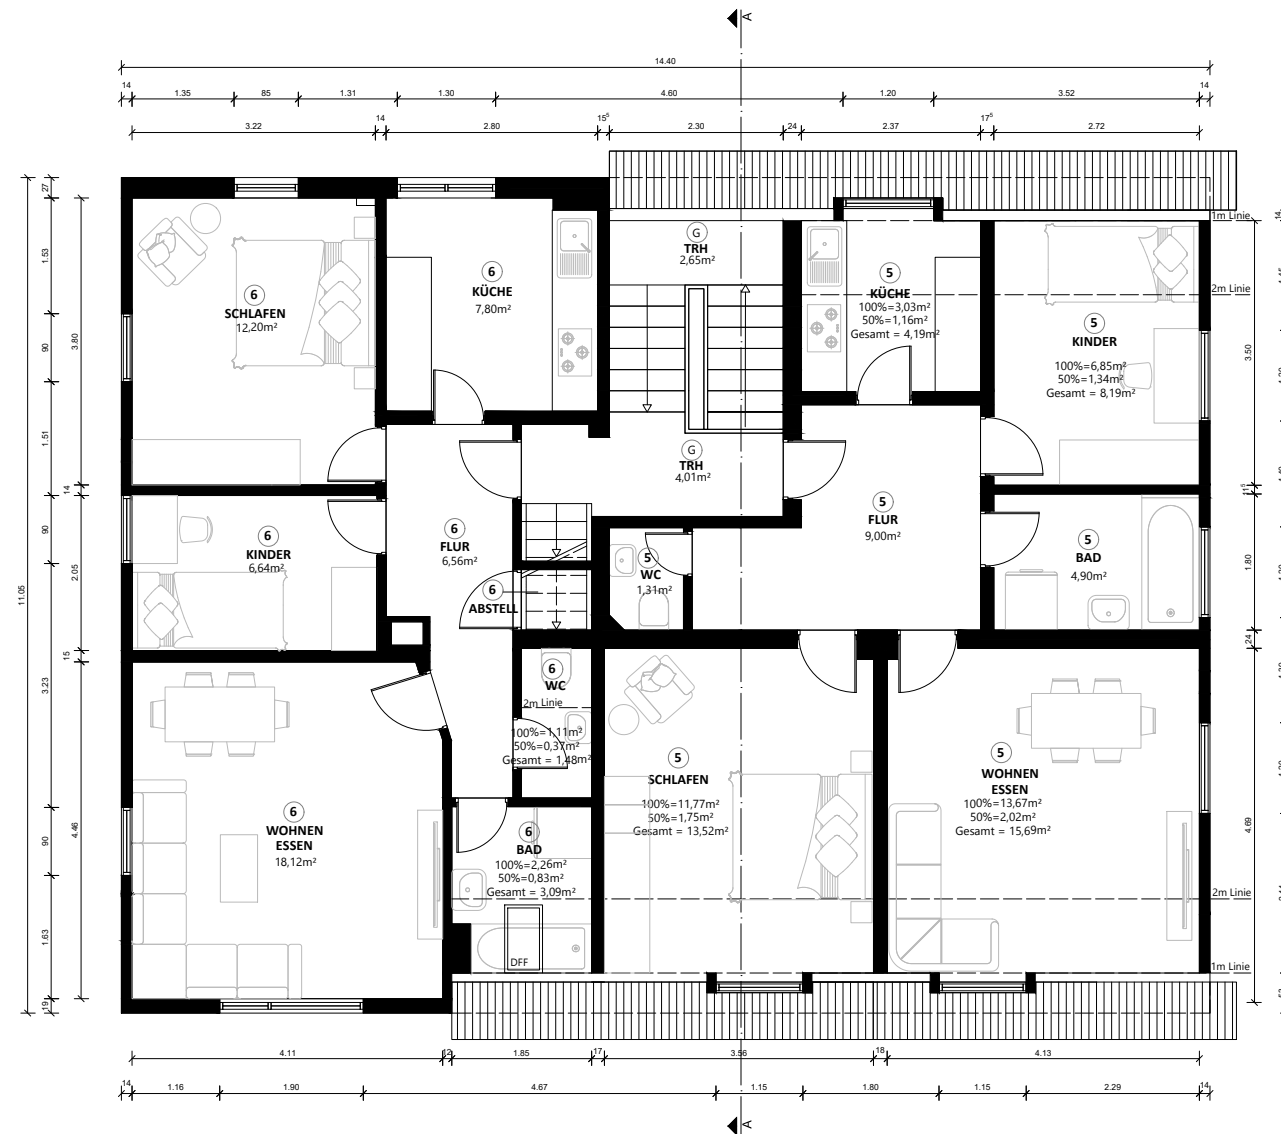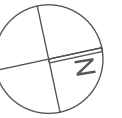

TEILUNGSPLAN

2.Obergeschoss

Art und Ort
des Vorhabens: Aufteilung eines bestehenden Wohngebäudes mit 7 Wohneinheiten
Roseggerstraße 9
73230 Kirchheim unter Teck
Flst.-Nr.: 278/3

Bauherr u.
Antragsteller: Württemberger Wohnkonzepte GmbH
Jesinger Str. 66
73230 Kirchheim unter Teck
Vertreten durch die Geschäftsführung: Dorothee Hahn & Marco Hans

Entwurfsverfasser:





jps architects
Jean Pierre Schellhaas
Architekt
Krokusstraße 3
71034 Böblingen
Mitglied der AKBW

jp@jps-architects.com
0157 / 39 22 86 22

M 1:100

Planstand: 08.06.2026

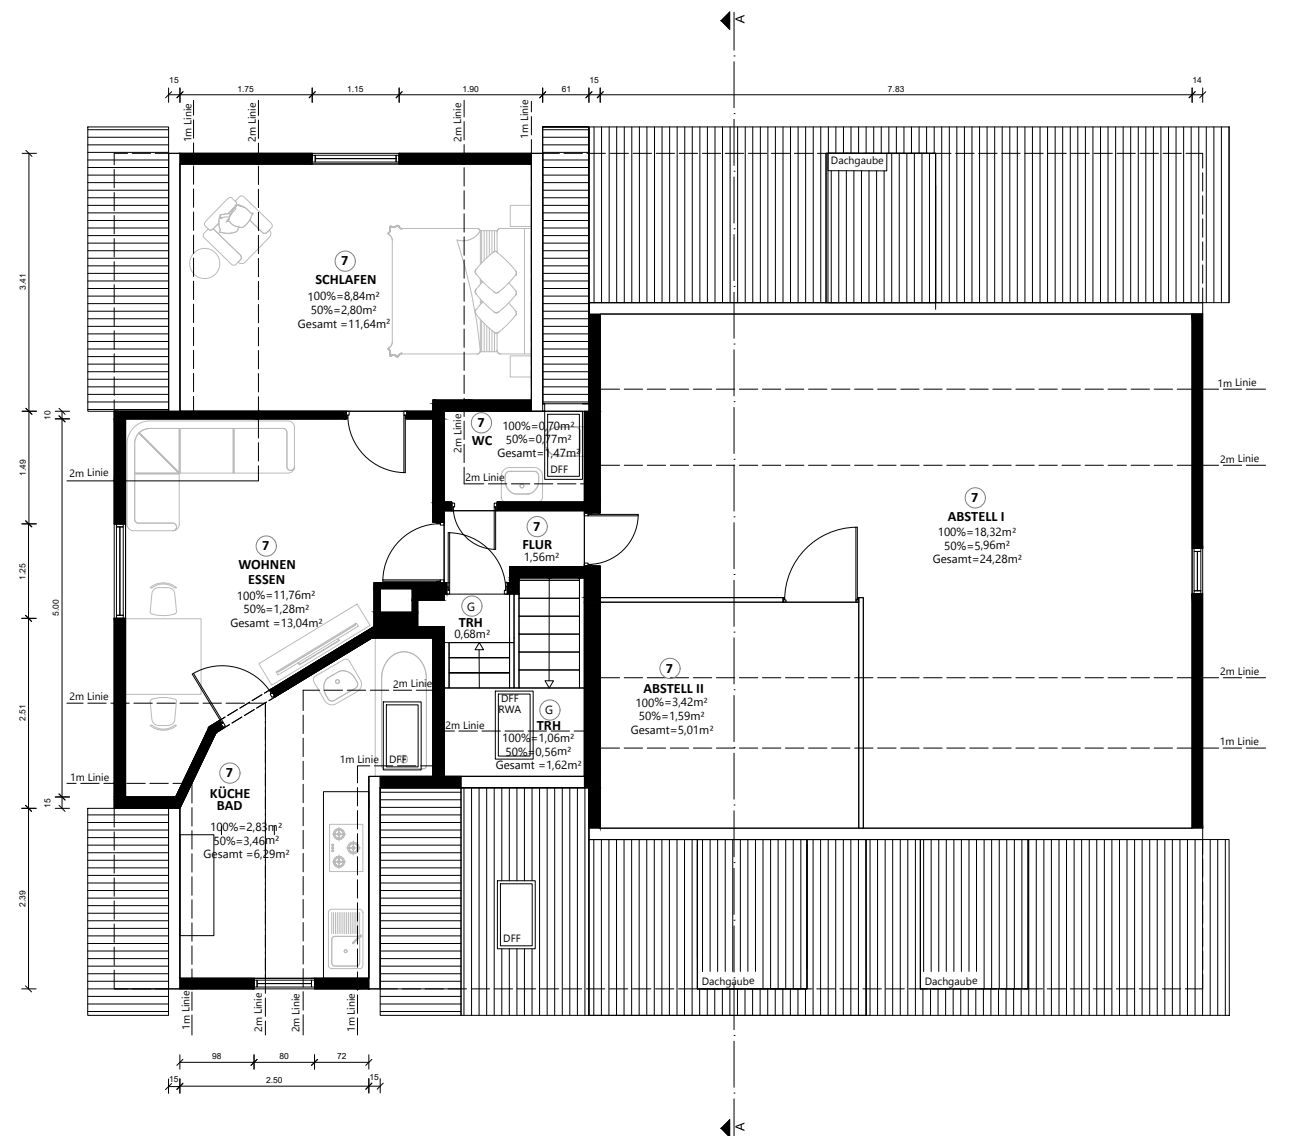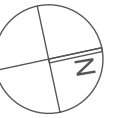

TEILUNGSPLAN

Dachgeschoss

Art und Ort
des Vorhabens: Aufteilung eines bestehenden Wohngebäudes mit 7 Wohneinheiten
Roseggerstraße 9
73230 Kirchheim unter Teck
Flst.-Nr.: 278/3

Bauherr u.
Antragsteller: Württemberger Wohnkonzepte GmbH
Jesinger Str. 66
73230 Kirchheim unter Teck
Vertreten durch die Geschäftsführung: Dorothee Hahn & Marco Hans

Entwurfsverfasser:





jps architects
Jean Pierre Schellhaas
Architekt
Krokusstraße 3
71034 Böblingen
Mitglied der AKBW

jp@jps-architects.com
0157 / 39 22 86 22

M 1:100

Planstand: 08.06.2026

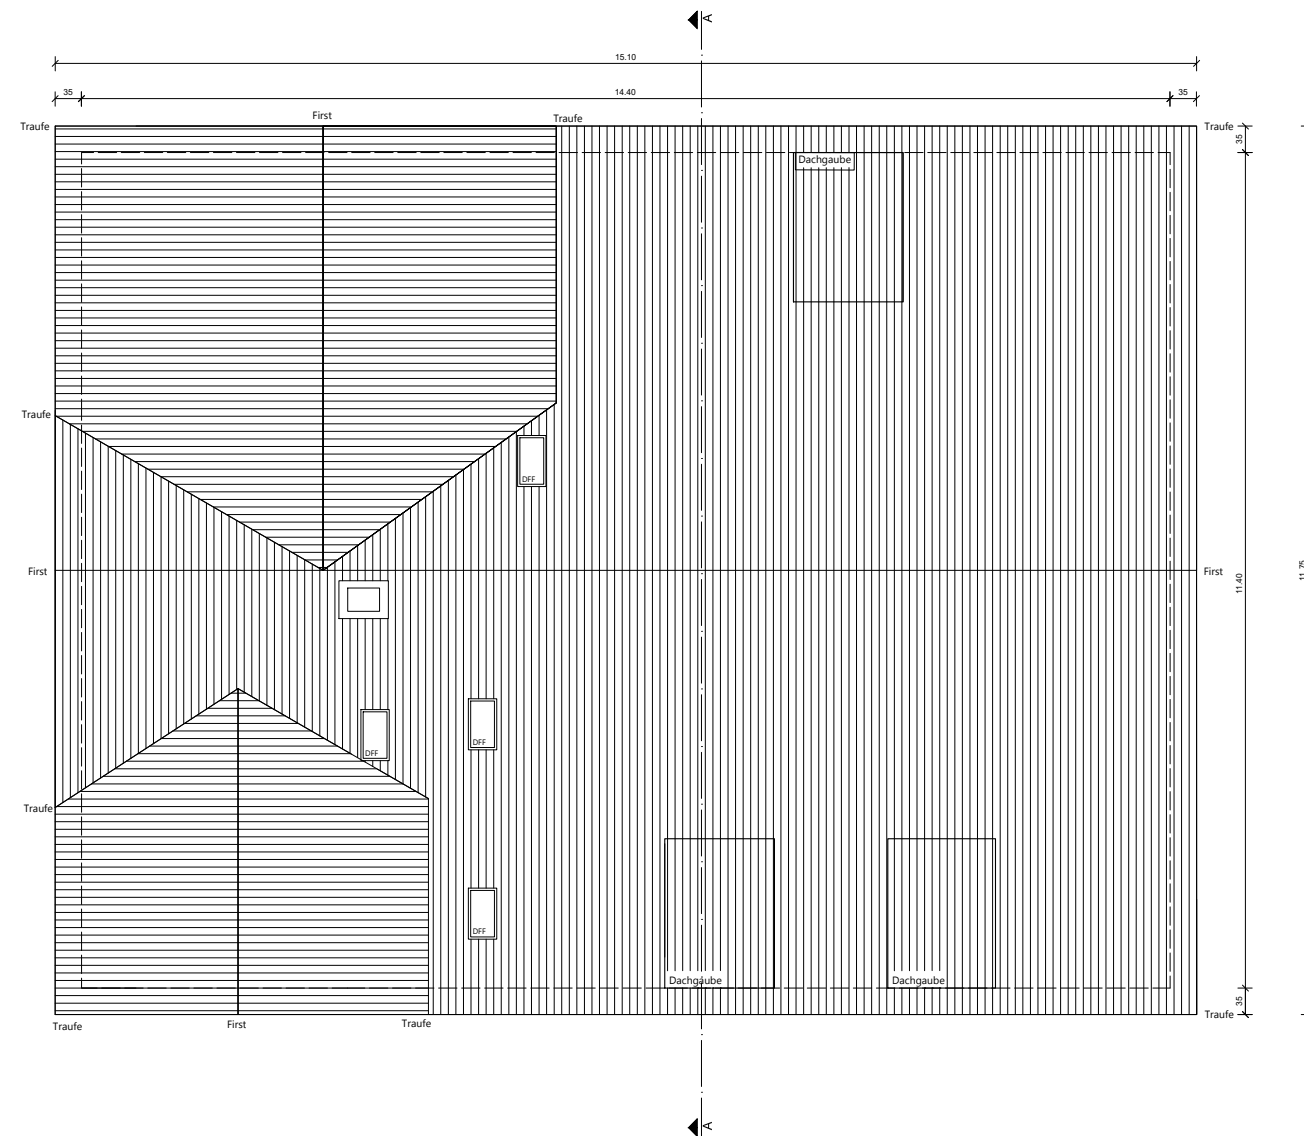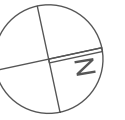

TEILUNGSPLAN

Dachaufsicht

Art und Ort
des Vorhabens: Aufteilung eines bestehenden Wohngebäudes mit 7 Wohneinheiten
Roseggerstraße 9
73230 Kirchheim unter Teck
Flst.-Nr.: 278/3

Bauherr u.
Antragsteller: Württemberger Wohnkonzepte GmbH
Jesinger Str. 66
73230 Kirchheim unter Teck
Vertreten durch die Geschäftsführung: Dorothee Hahn & Marco Hans


Entwurfsverfasser:
jps architects
Jean Pierre Schellhaas
Architekt
Krokusstraße 3
71034 Böblingen
Mitglied der AKBW



jp@jps-architects.com
0157 / 39 22 86 22

M 1:100

Planstand: 08.06.2026

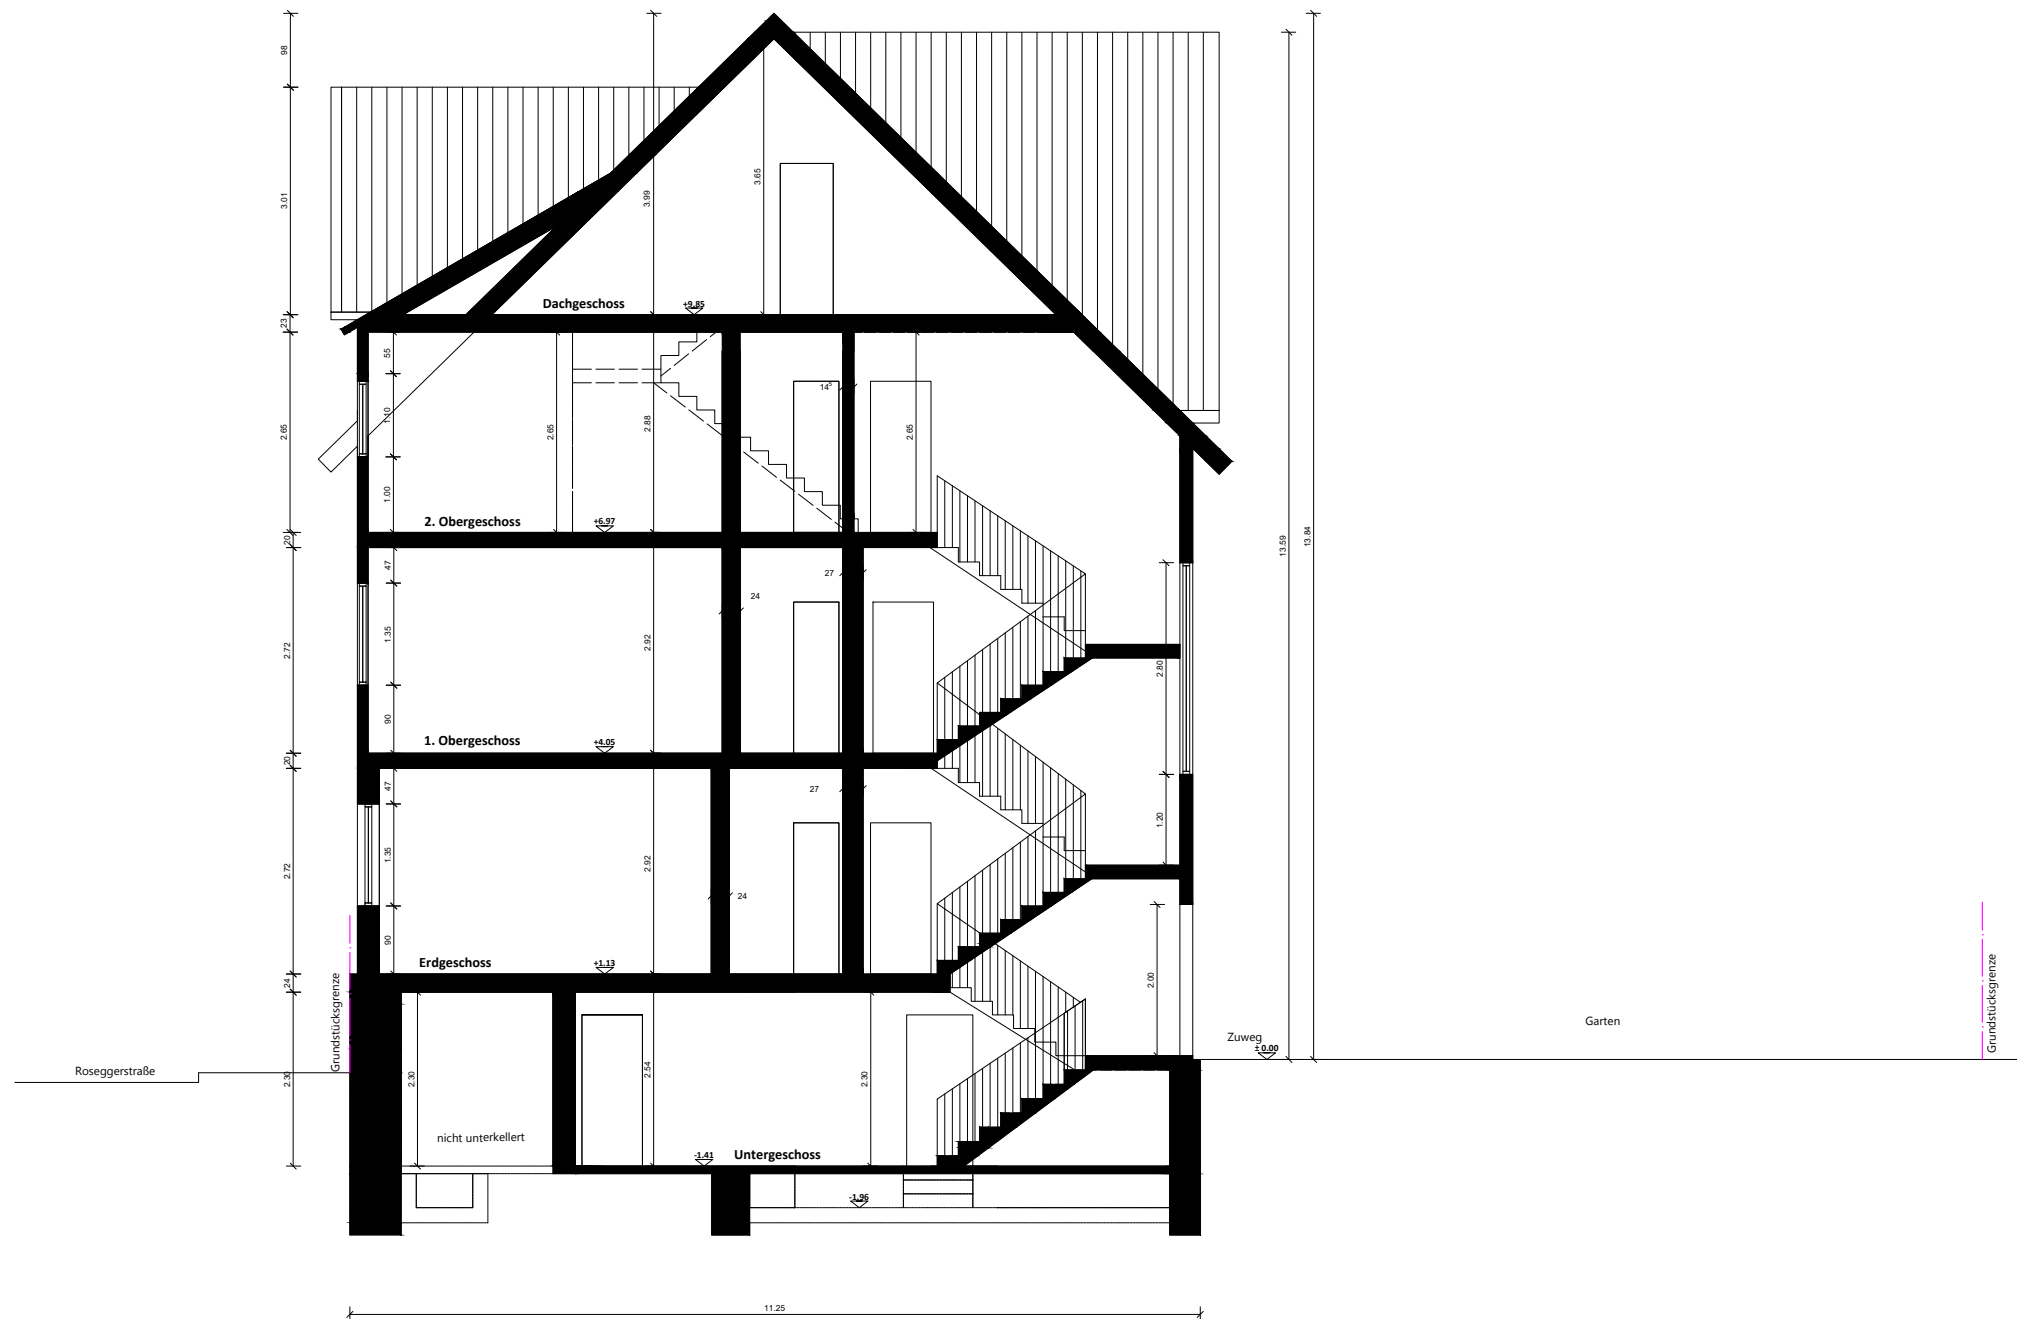

TEILUNGSPLAN

Schnitt A-A


Art und Ort
des Vorhabens:

Aufteilung eines bestehenden Wohngebäudes mit 7 Wohneinheiten
Roseggerstraße 9
73230 Kirchheim unter Teck
Flst.-Nr.: 278/3

Bauherr u.
Antragsteller:

Württembergischer Wohnkonzepte GmbH
Jesinger Str. 66
73230 Kirchheim unter Teck
Vertreten durch die Geschäftsführung: Dorothee Hahn & Marco Hans

Entwurfsverfasser:

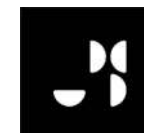


jps architects
Jean Pierre Schellhaas
Architekt
Krokusstraße 3
71034 Böblingen
Mitglied der AKBW

jp@jps-architects.com
0157 / 39 22 86 22

M 1:100

Planstand: 08.06.2026

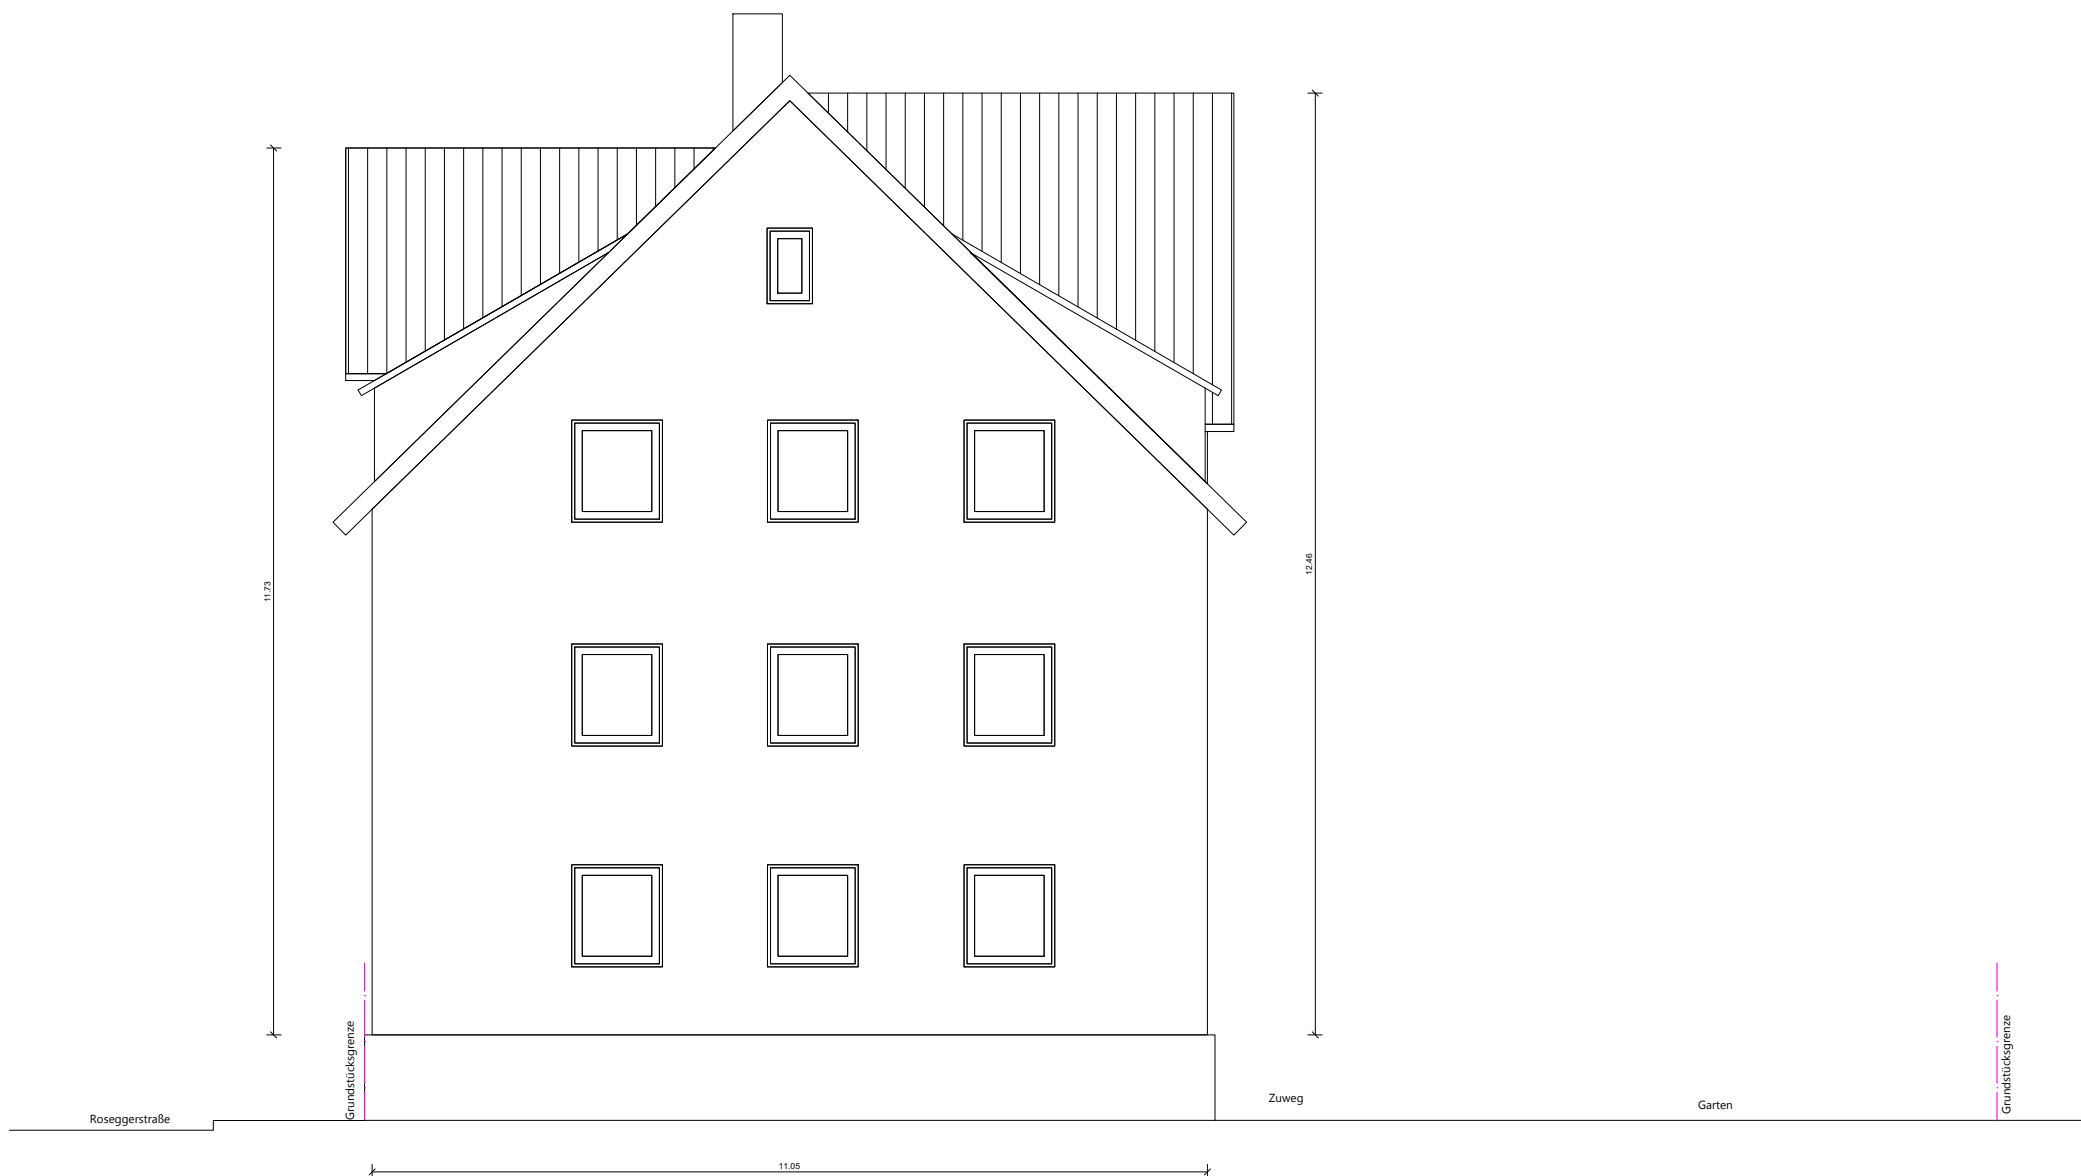

TEILUNGSPLAN

Ansicht Nord

Art und Ort
des Vorhabens: Aufteilung eines bestehenden Wohngebäudes mit 7 Wohneinheiten
Roseggerstraße 9
73230 Kirchheim unter Teck
Flst.-Nr.: 278/3

Bauherr u.
Antragsteller: Württemberger Wohnkonzepte GmbH
Jesinger Str. 66
73230 Kirchheim unter Teck
Vertreten durch die Geschäftsführung: Dorothee Hahn & Marco Hahn

Entwurfsverfasser:



jps architects
Jean Pierre Schellhaas
Architekt
Krokusstraße 3
71034 Böblingen
Mitglied der AKBW

jp@jps-architects.com
0157 / 39 22 86 22


M 1:100

Planstand: 08.06.2026




TEILUNGSPLAN

Ansicht Süd

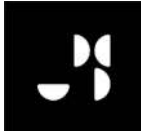Art und Ort des Vorhabens:	Aufteilung eines bestehenden Wohngebäudes mit 7 Wohneinheiten	
	Roseggerstraße 9 73230 Kirchheim unter Teck Flst.-Nr.: 278/3	
Bauherr u. Antragsteller:	Württembergischer Wohnkonzepte GmbH Jesinger Str. 66 73230 Kirchheim unter Teck Vertreten durch die Geschäftsführung: Dorothee Hahn & Marco Hans	
		
Entwurfsverfasser:		
	jps architects Jean Pierre Schellhaas Architekt Krokusstraße 3 71034 Böblingen Mitglied der AKBW jp@jps-architects.com 0157 / 39 22 86 22	
M 1:100		

Planstand: 08.06.2026

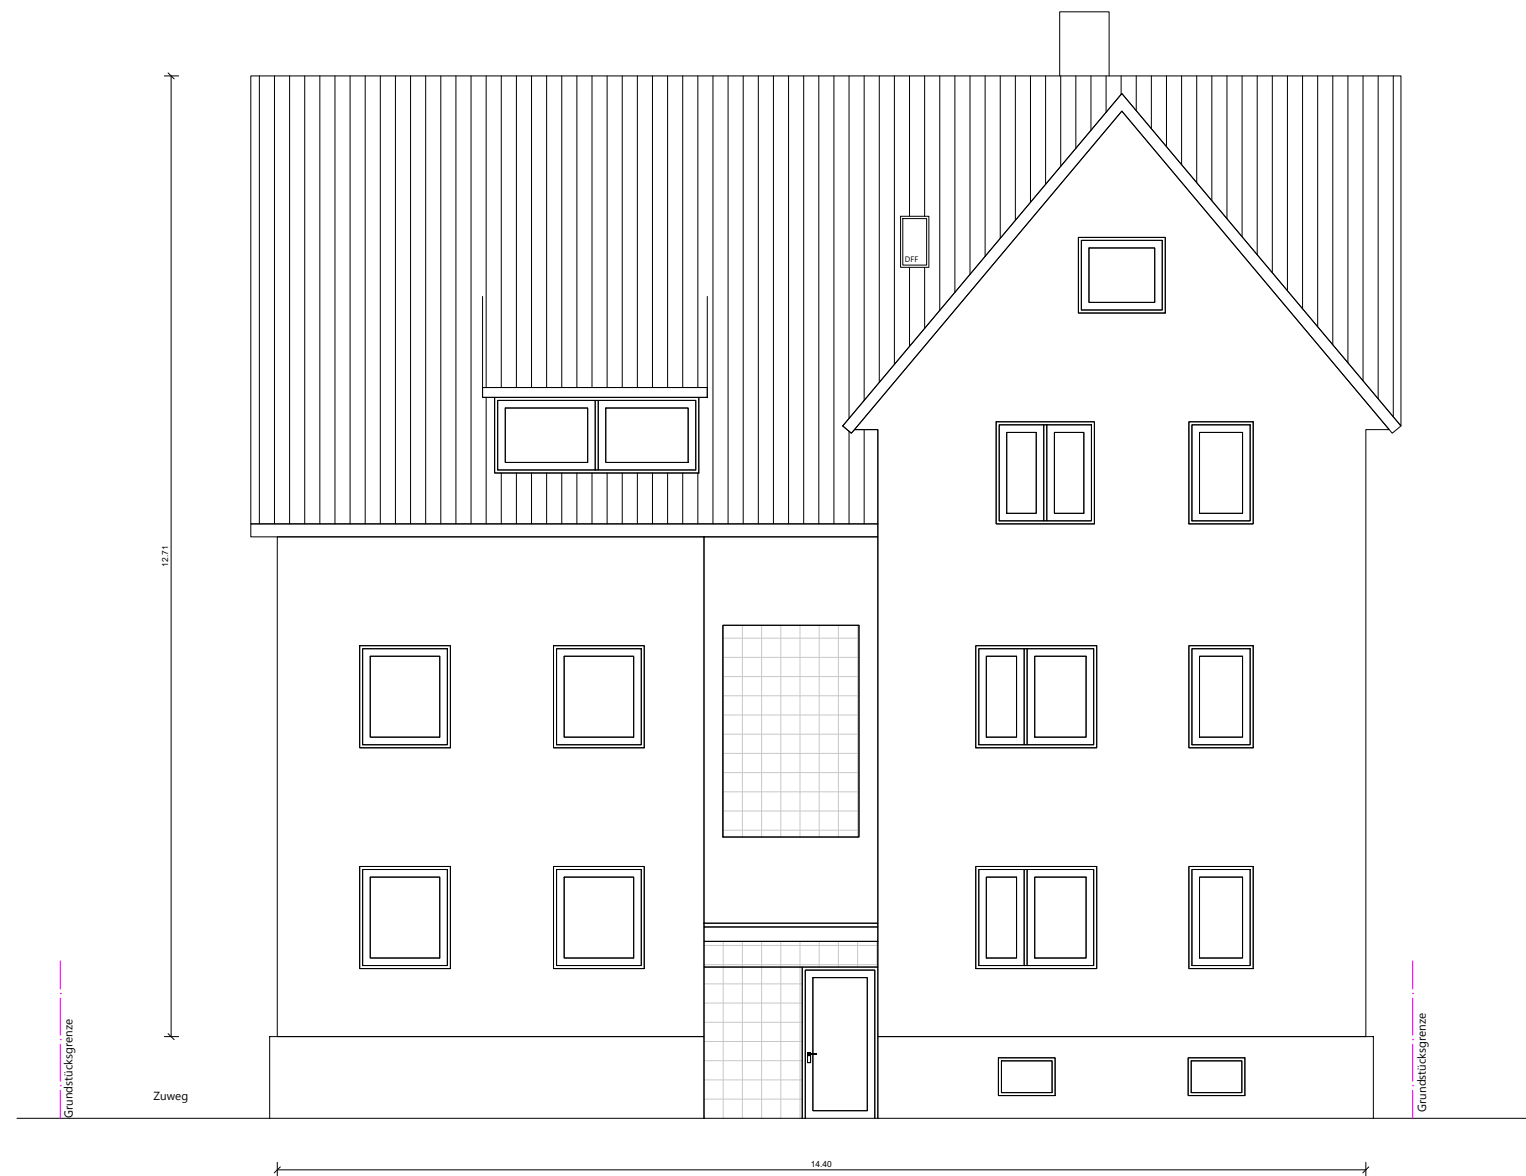

TEILUNGSPLAN

Ansicht West

Art und Ort
des Vorhabens: Aufteilung eines bestehenden Wohngebäudes mit 7 Wohneinheiten
Roseggerstraße 9
73230 Kirchheim unter Teck
Flst.-Nr.: 278/3

Bauherr u.
Antragsteller: Württemberger Wohnkonzepte GmbH
Jesinger Str. 66
73230 Kirchheim unter Teck
Vertreten durch die Geschäftsführung: Dorothee Hahn & Marco Hans

Entwurfsverfasser:




jps architects
Jean Pierre Schellhaas
Architekt
Krokusstraße 3
71034 Böblingen
Mitglied der AKBW

jp@jps-architects.com
0157 / 39 22 86 22

M 1:100

Planstand: 08.06.2026

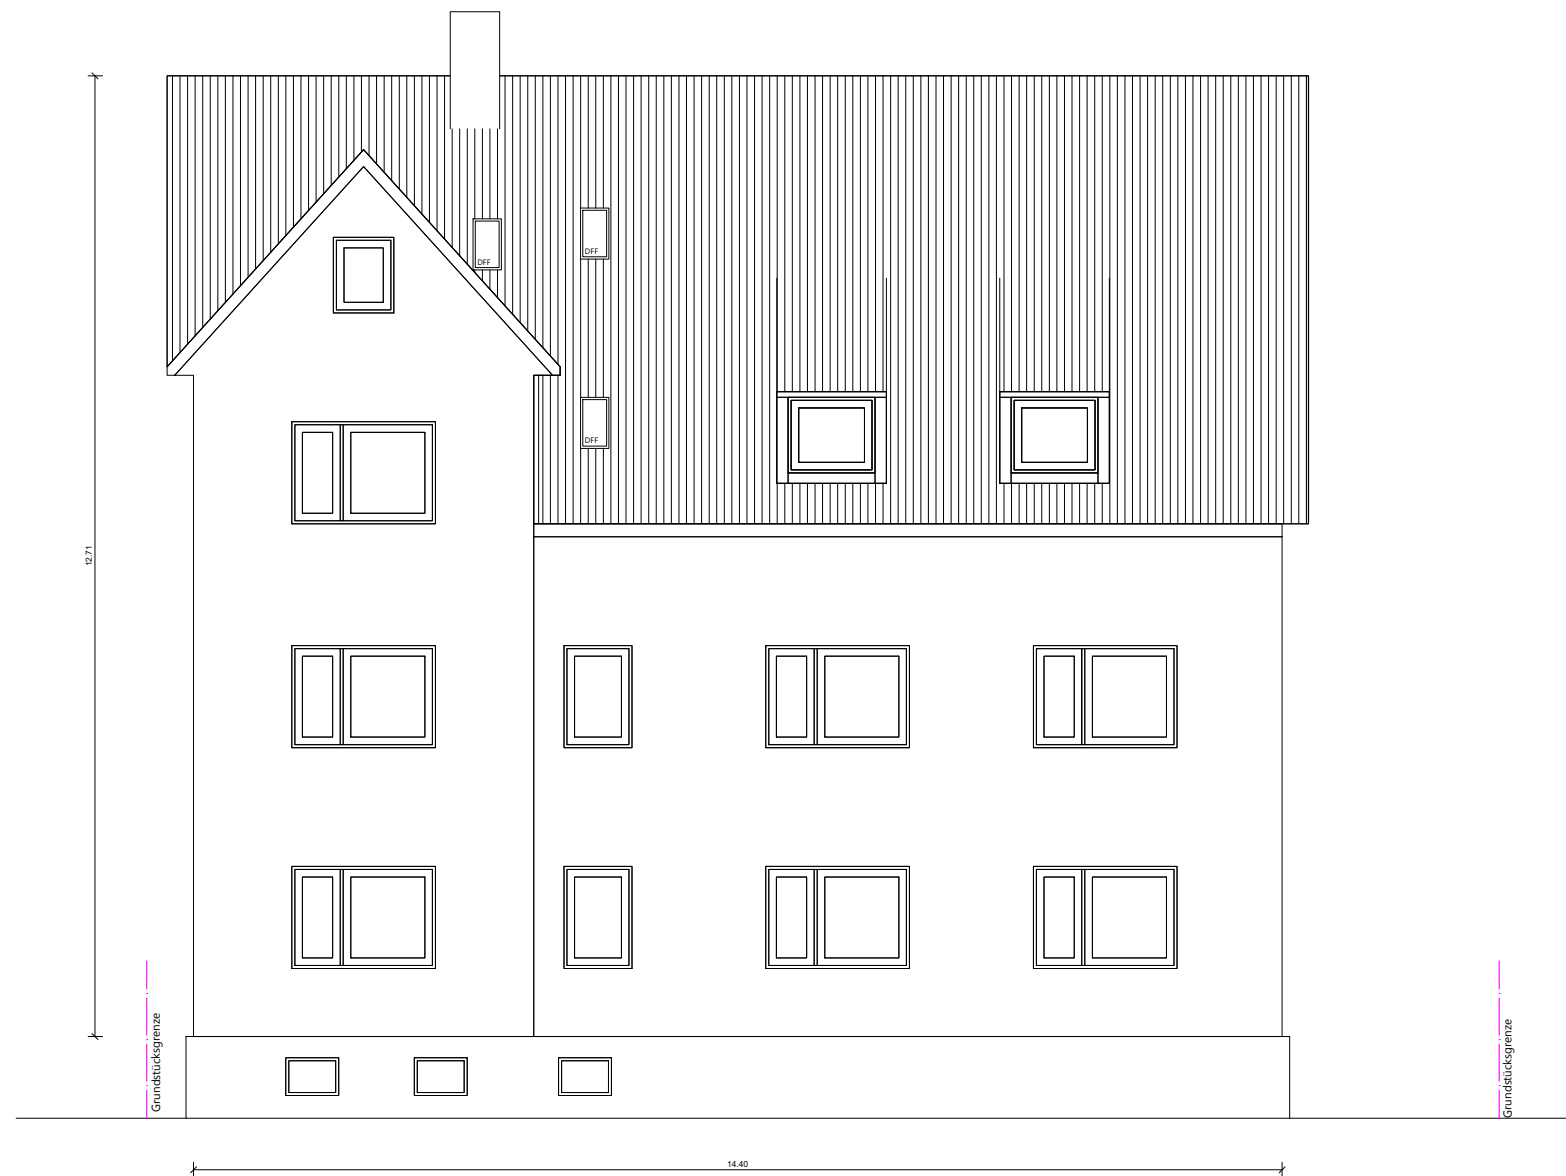

TEILUNGSPLAN

Ansicht Ost

Art und Ort
des Vorhabens: Aufteilung eines bestehenden Wohngebäudes mit 7 Wohneinheiten
Roseggerstraße 9
73230 Kirchheim unter Teck
Flst.-Nr.: 278/3

Bauherr u.
Antragsteller: Württemberger Wohnkonzepte GmbH
Jesinger Str. 66
73230 Kirchheim unter Teck
Vertreten durch die Geschäftsführung: Dorothee Hahn & Marco Hans

Entwurfsverfasser:



jps architects
Jean Pierre Schellhaas
Architekt
Krokusstraße 3
71034 Böblingen
Mitglied der AKBW

jp@jps-architects.com
0157 / 39 22 86 22

M 1:100

Planstand: 08.06.2026