

Stadt - Gemeinde: Kirchheim unter Teck

Landkreis: Nürtingen

Baugesuch

Bauherr Martin Hanke, Ingenieur
Kirchheim unter Teck
Paradiesstraße 21

Bauvorhaben: Umbau des bestehenden
Wohngebäudes

Grundstück: Roseggerstrasse 9

Architekt Fritz Allmendinger
Freier Architekt
Altbach/Neckar

BAUTAGEBUCH
19 70 Nr. 430

LAGEPLAN


KREIS: NÜRTINGEN
STADT: KIRCHHEIM-TECK
MARKUNG:

MASSTAB 1:500



O.W. 102 KLOSTERSTR.

O.W. 140

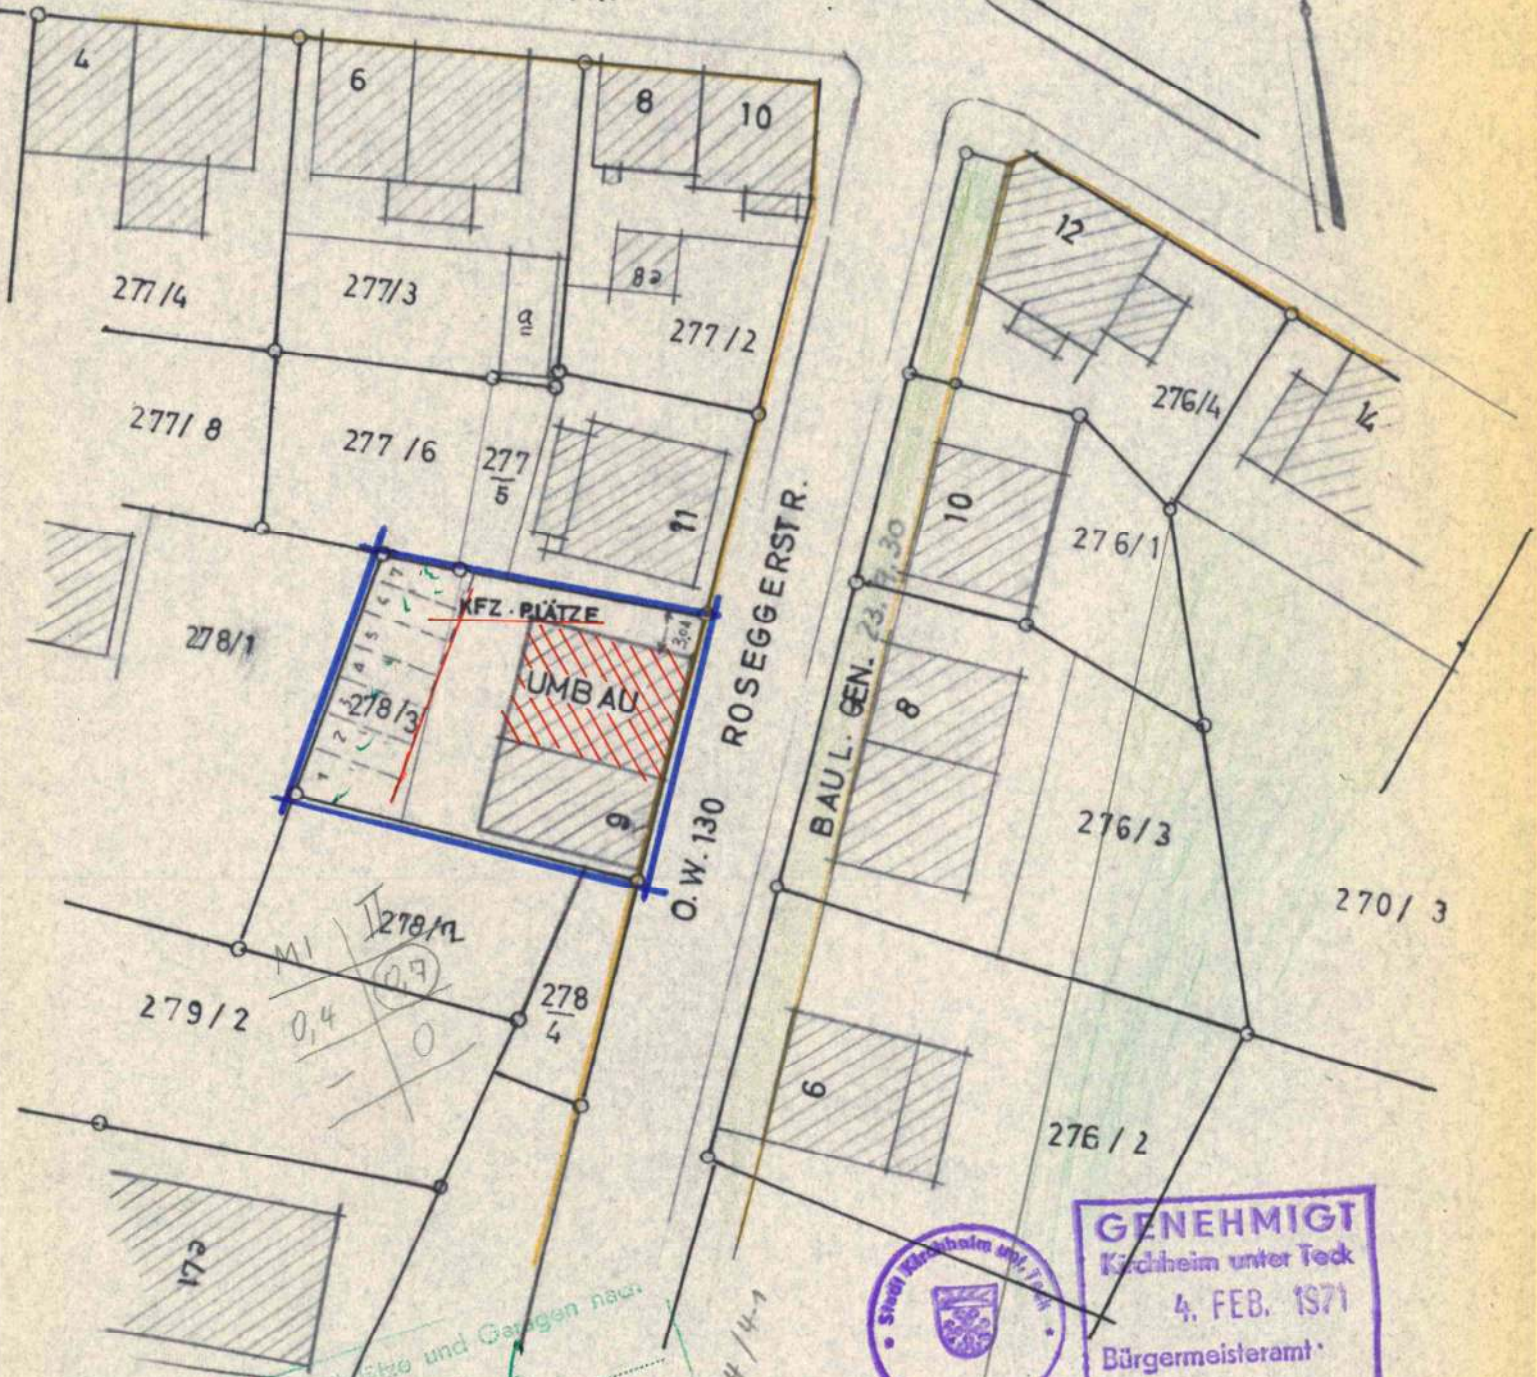

Kfz-Einstellplätze und Garagen nach
§ 3 der L.O. u. O.
Erforderlich:
vorhanden:
neu zu schaffen:




GENEHMIGT
Kirchheim unter Teck
4. FEB. 1971
Bürgermeisteramt

GEFERTIGT: 5.12.70

Altmendinger
FRITZ ALLMENDINGER
ARCHITEKT
7305 ALTBACH
UMLANDSTR. 11

KIRCHHEIM - TECK UMBAU ROSEGGGERSTR. 9

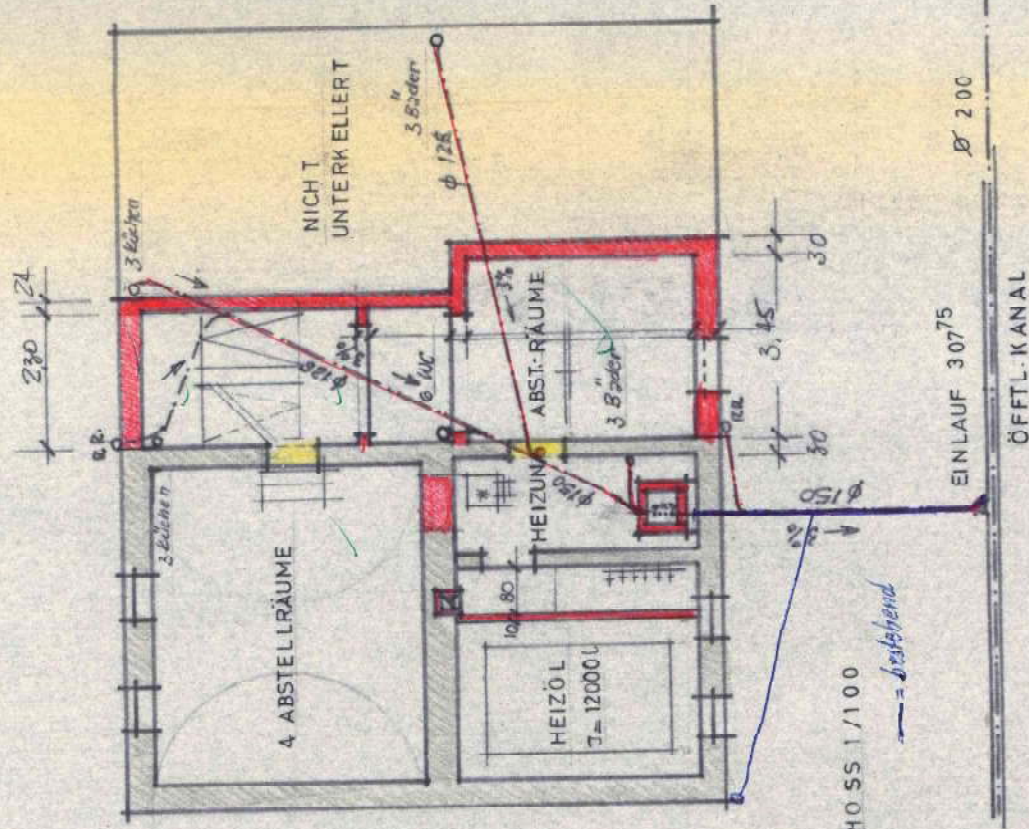


DAS UNTERGESCHOSS 1/100

— = bestehend


ANERKANNT:

BAUHERR:

Paul Lohr

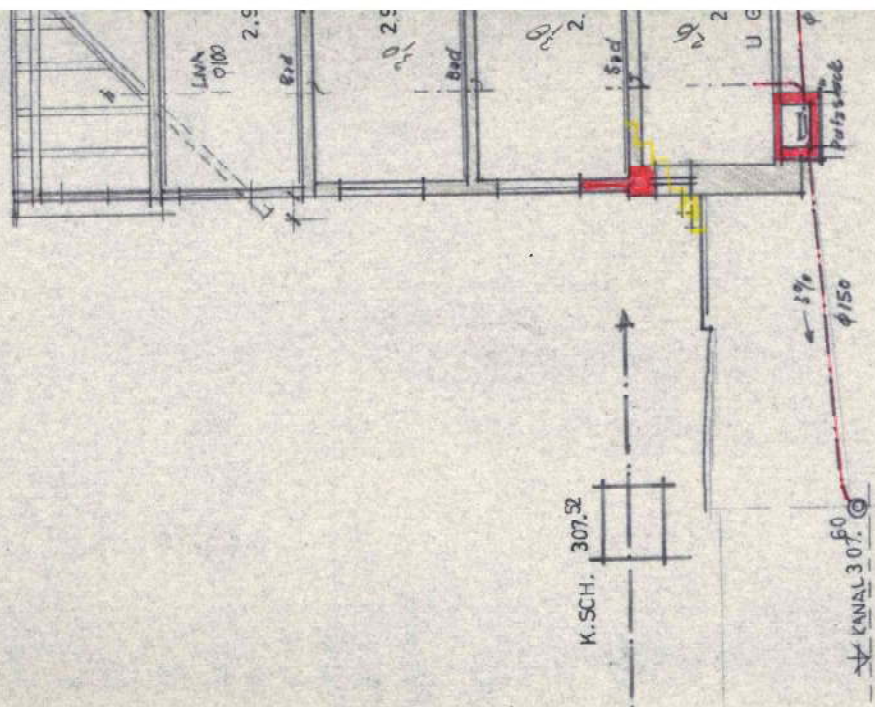

DER SCHNITT 1/100

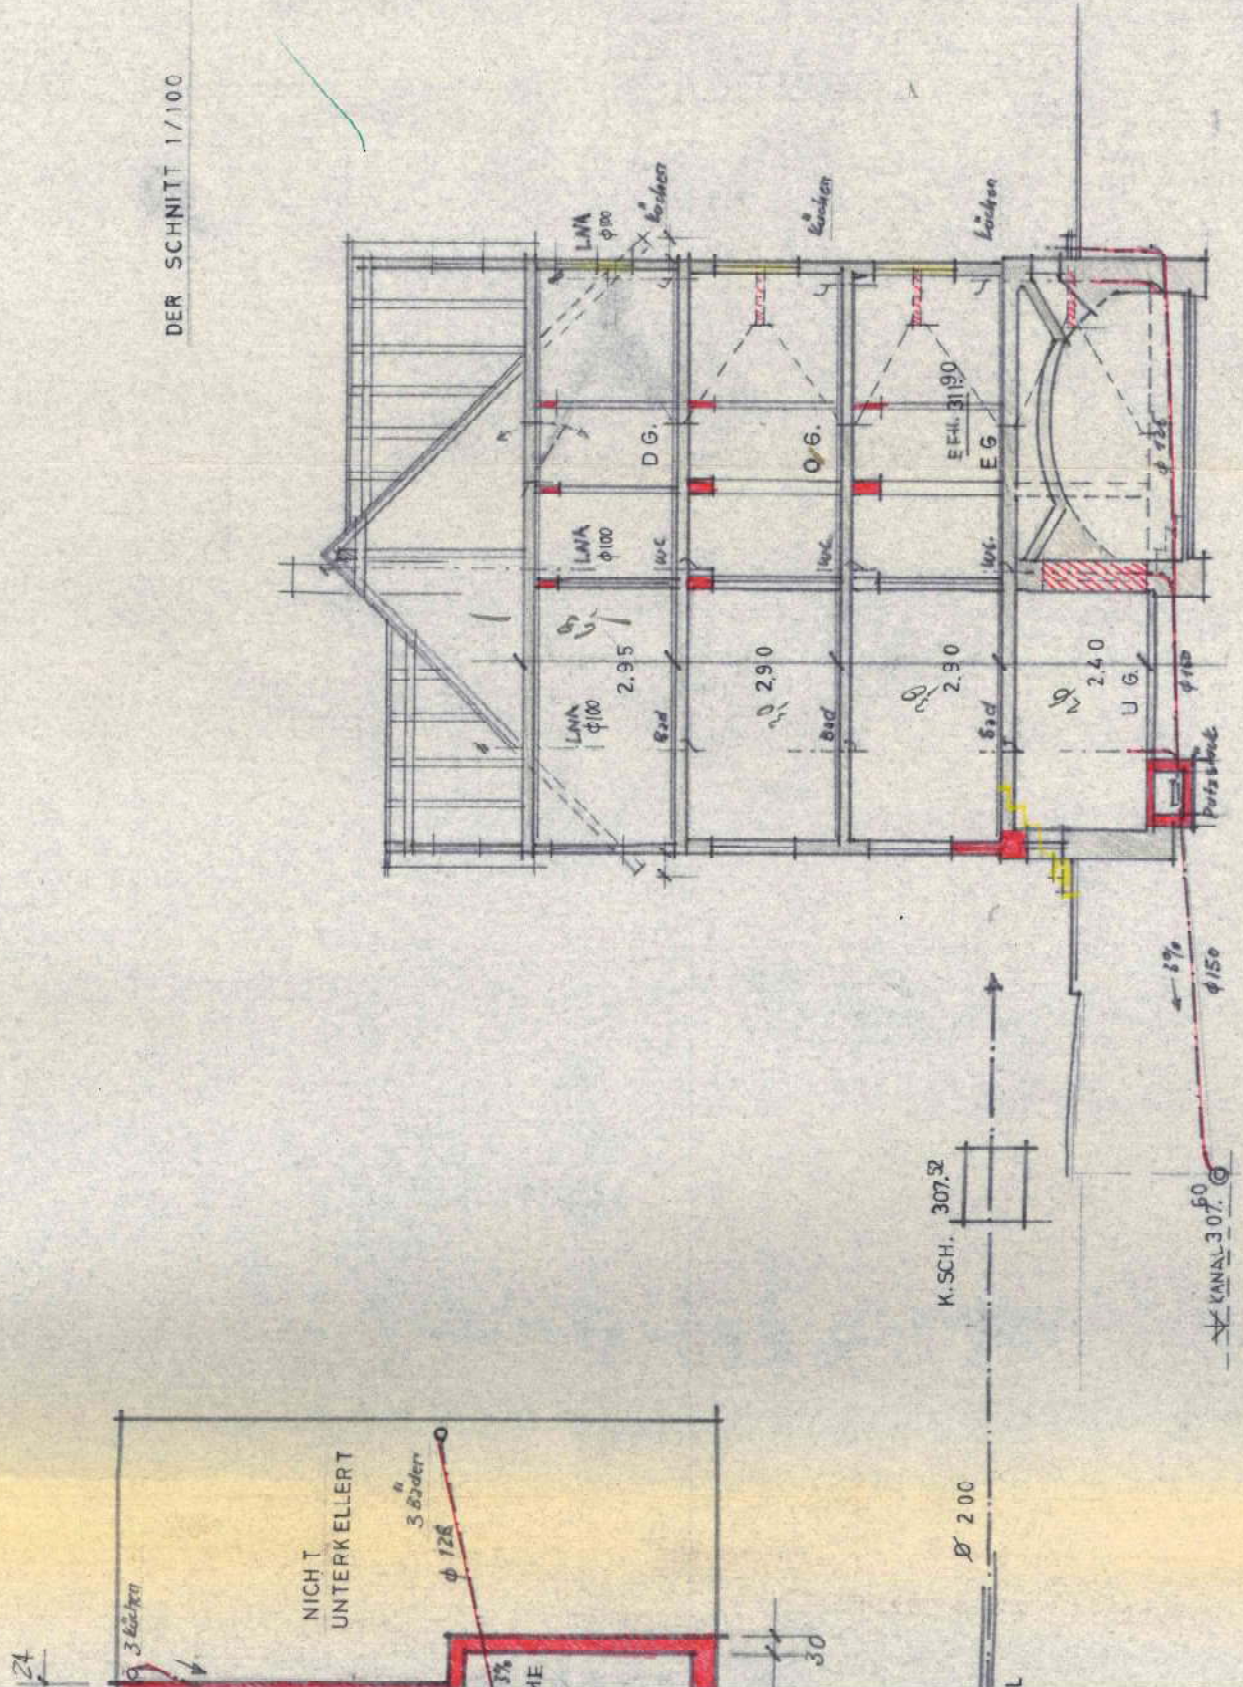


GENEHMIGT
Kirchheim unter Teck
4. FEB. 1971
Bürgermeisteramt



GEFERTIGT: 5.12.70

ARCHITEKT:

Reimer P.

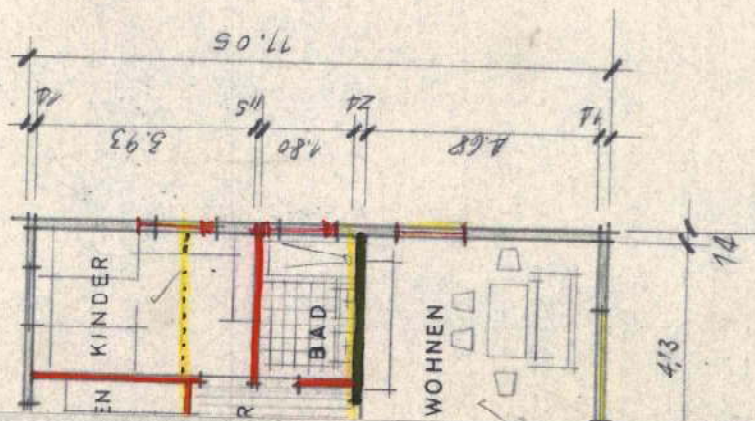


ARCHI TEK:

Allen

DAS DACHGESCHOSS 1/100



KIRCHHEIM-TECK

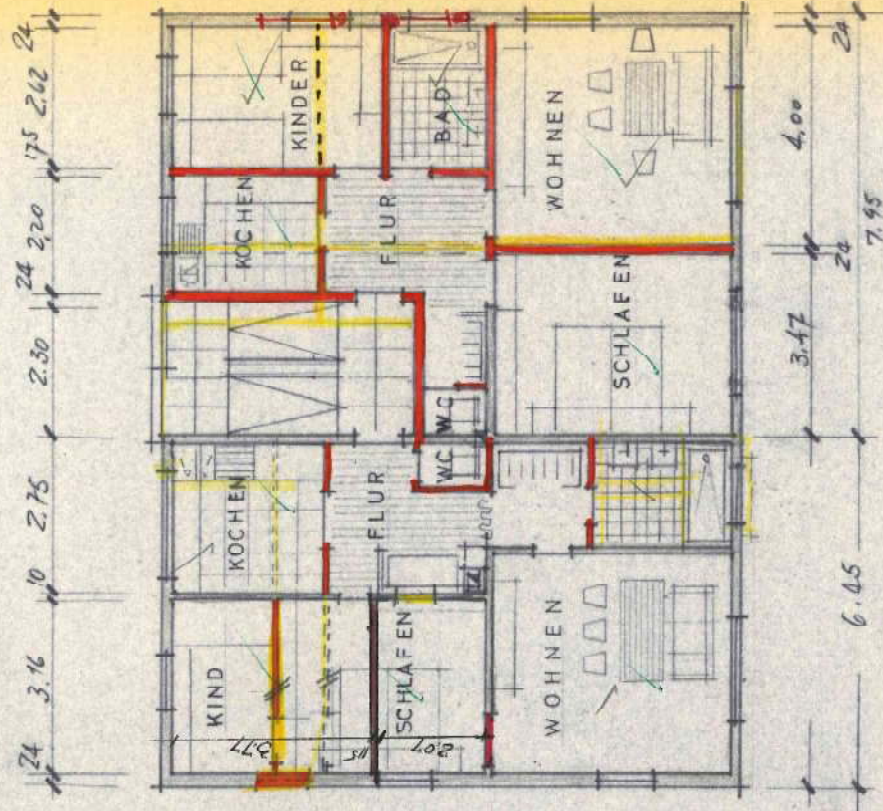

— 147 —


ANERKANNT:

BAILLIERE

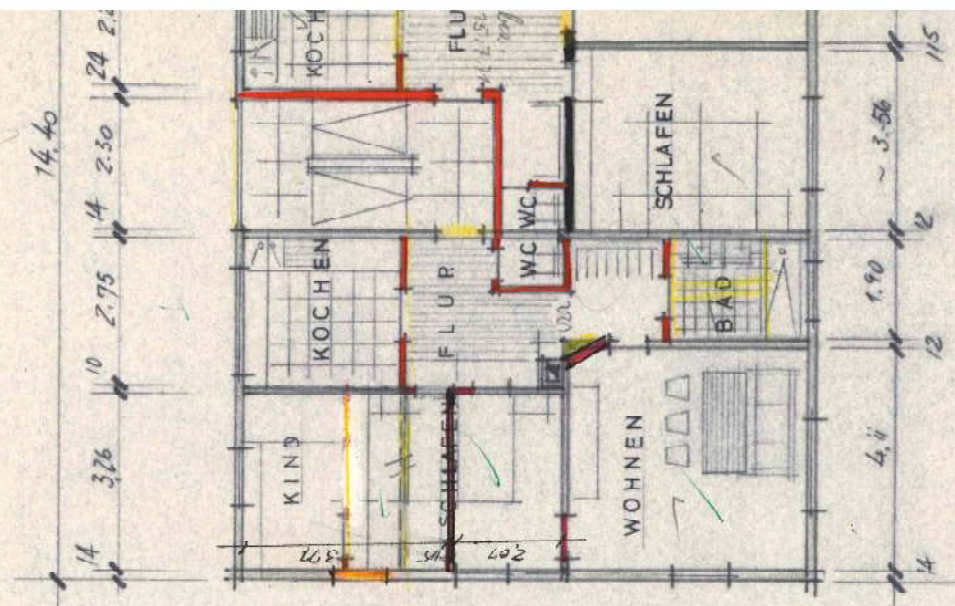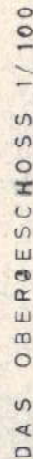

— 147 —

KIRCHHEIM-TECK
UMBAU ROSEGGGERSTR. 9

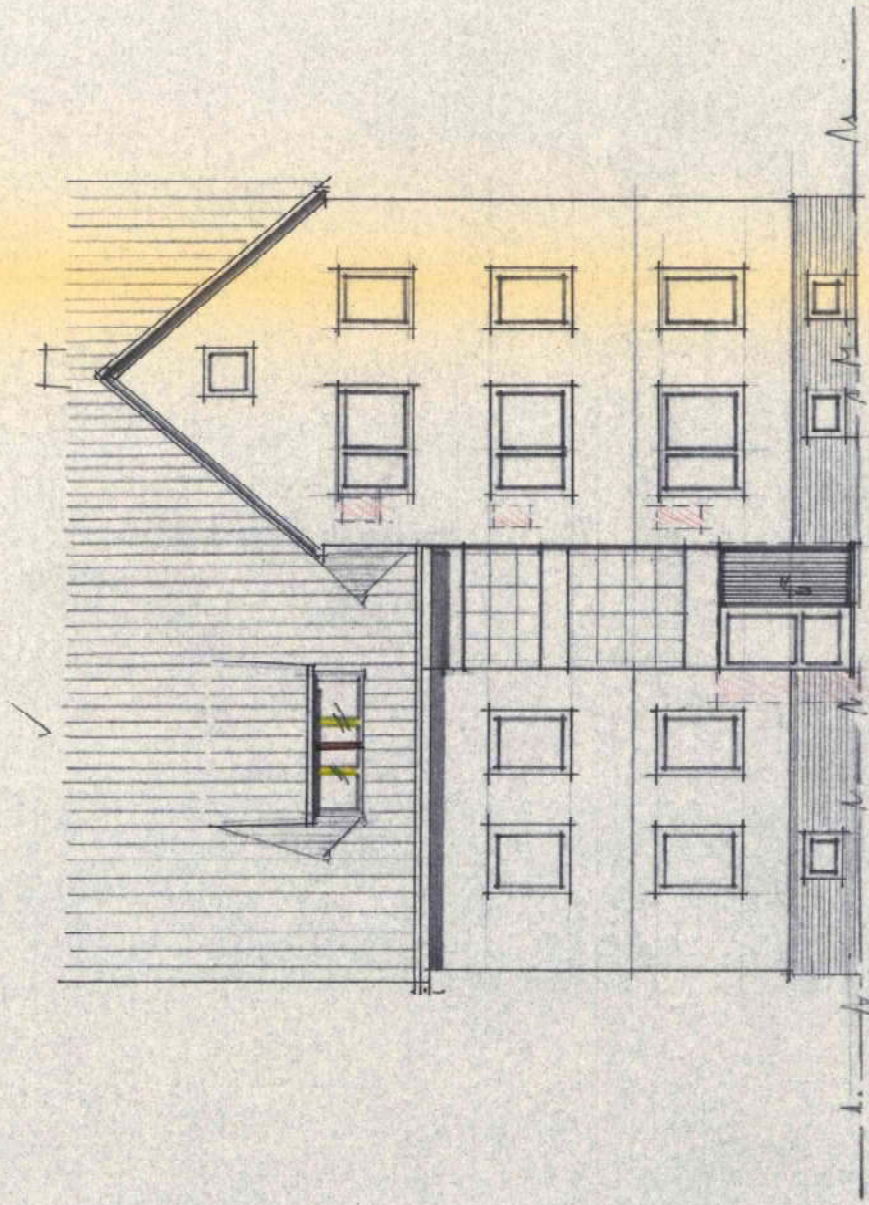


DIE WESTSEITE 1/100

ANERKANNT:
BAUHERRE

Paul Kauer

DIE NORDSEITE 1/100

STR. 9

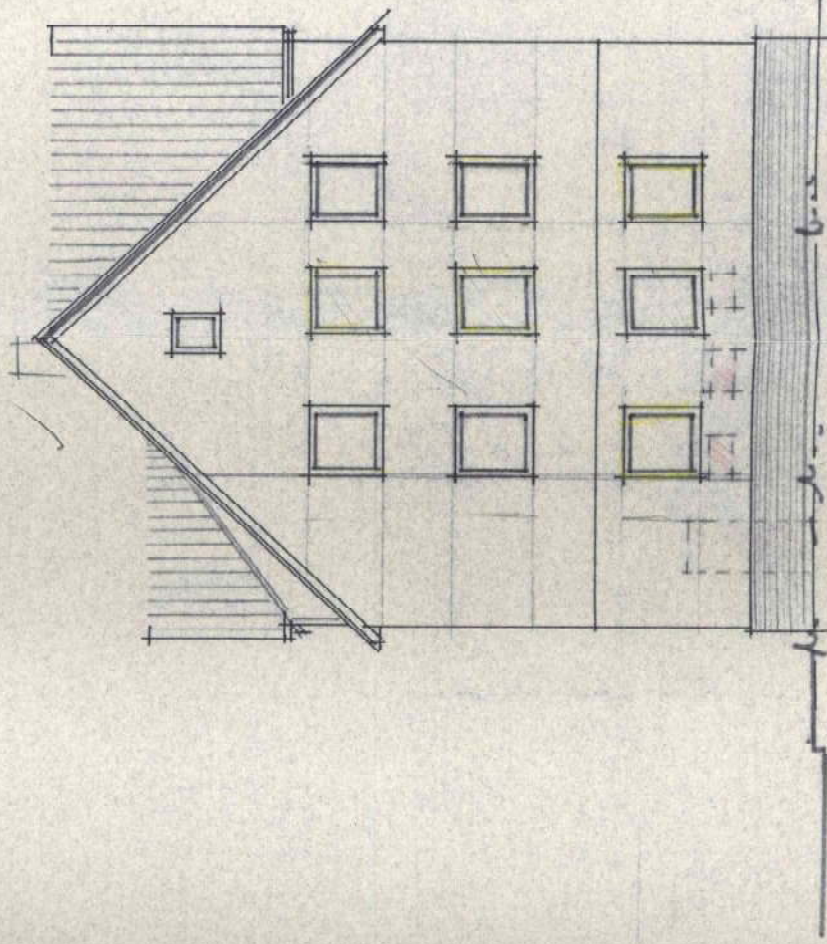

DIE NORDSEITE 1/100

GENEHMIGT
Kirchheim unter Teck
4. FEB. 1971
Bürgermeisteramt



GEFERTIGT: 5.12.70
ARCHITEKT:

Almuth S.

KIRCHHEIM - TECK
UMBAU ROSEGGERSTR. 9



OSTSEITE 1 / 100

ANERKANNT:

BAUHERR: *Carl Lenz*

GEFERTIGT: 5.12.70

ARCHITEKT:

Altmann

GENEHMIGT

Kirchheim unter Teck

4. FEB. 1971

Bürgermeisteramt

